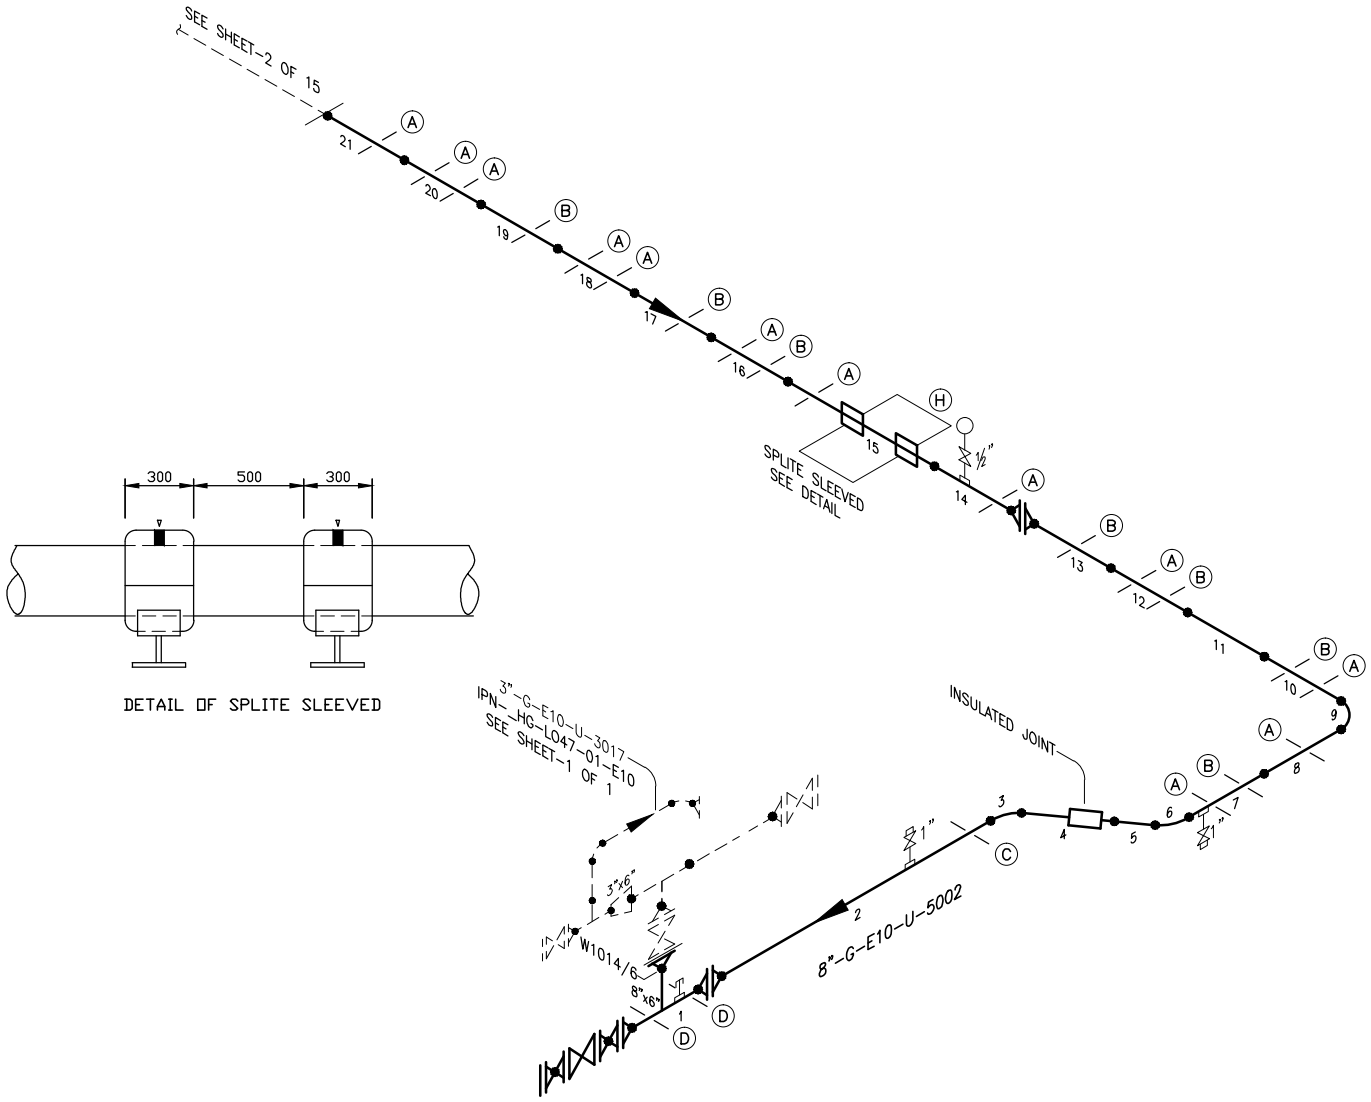
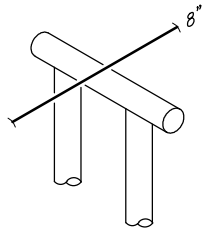
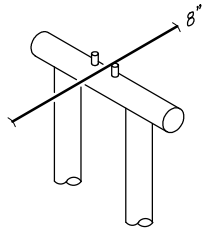
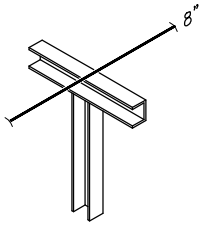
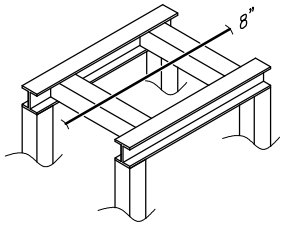
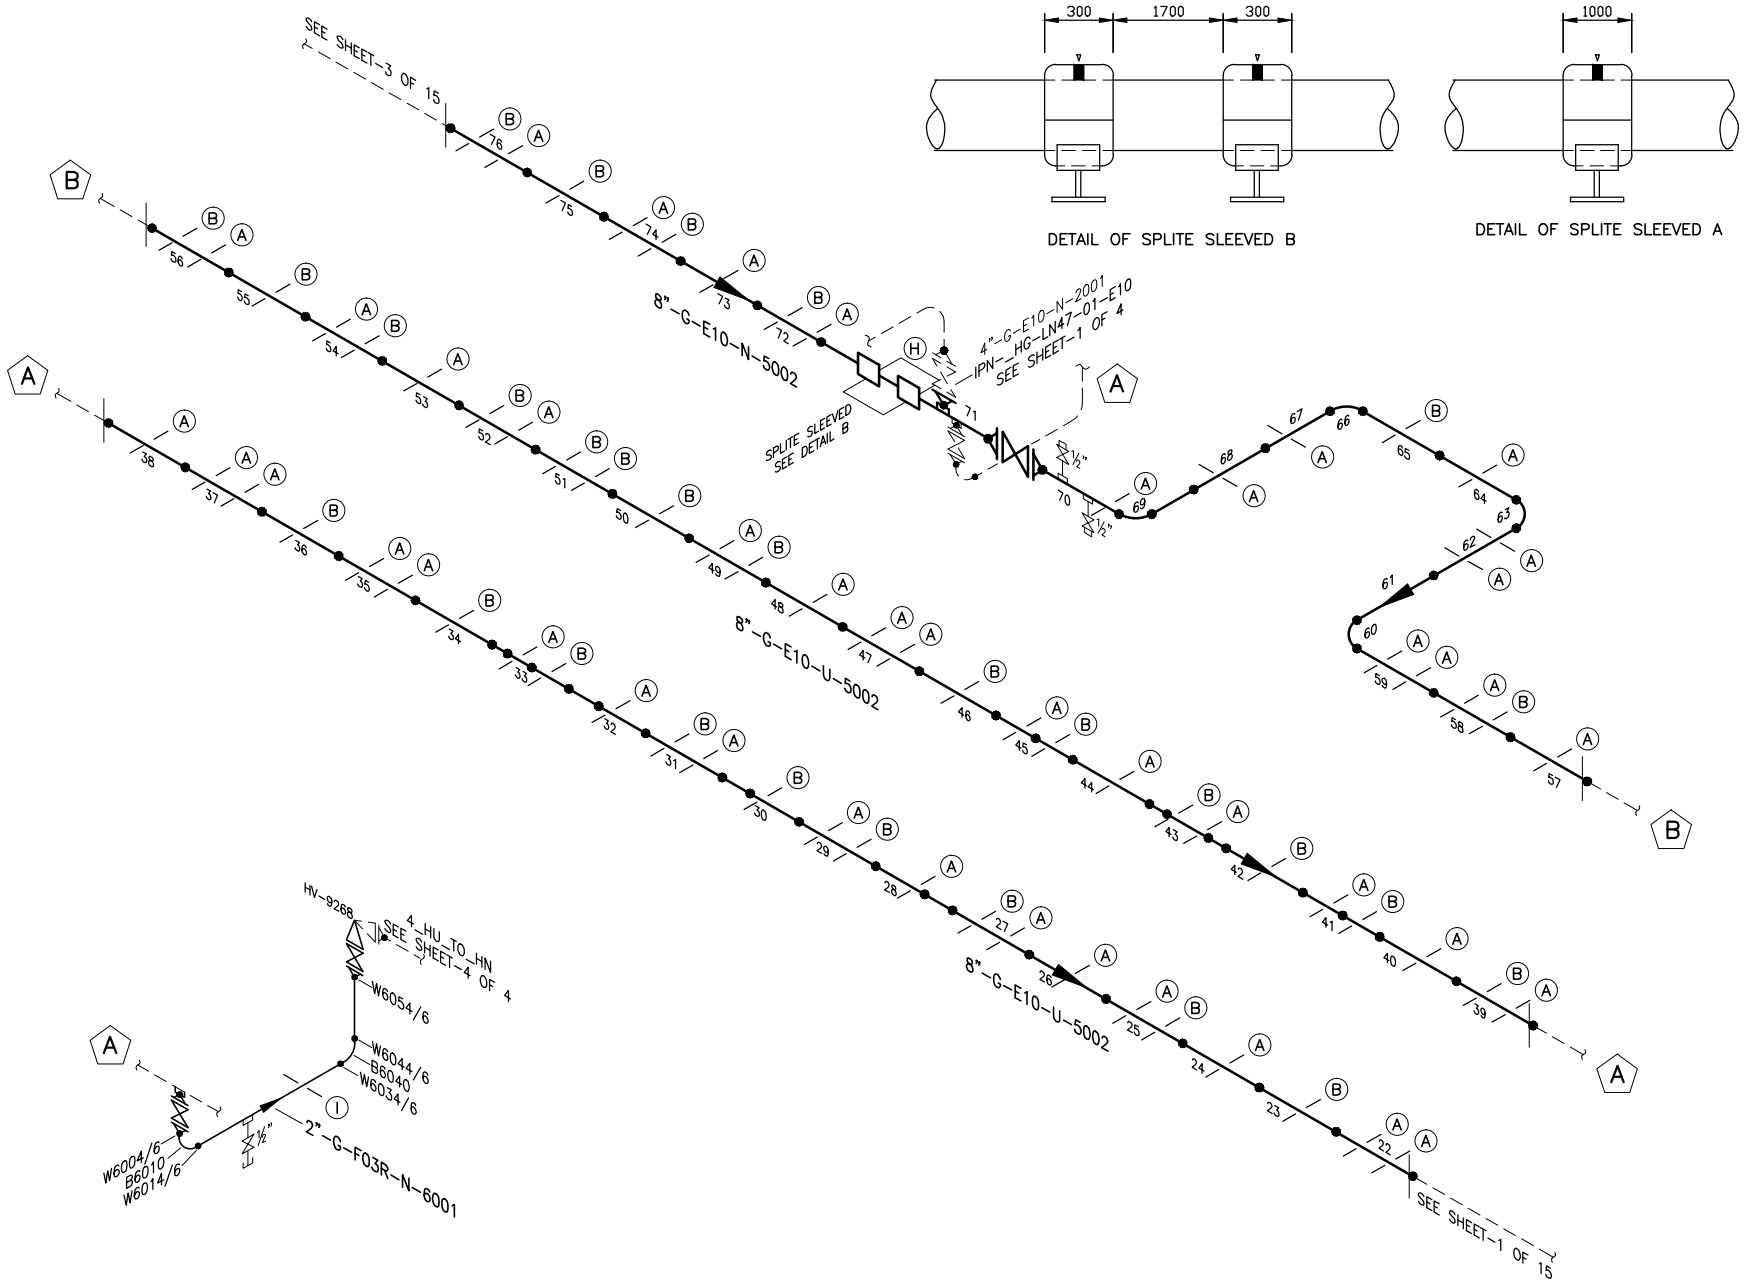



| No | SUPPORT DETAIL |
|---|---|
| A |  |
| B |  |
| C |  |
| H |  |

| CODE | DESCRIPTION |
|---|---|
| AA | NO SPACE FOR SCANNING |
| AC | BLOCKED BY EQUIPMENT |
| AD | BLOCKED BY SUPPORT (cannot be removed) |
| BA | HIGH LOCATION |
| BB | UNDER DECK |
| BC | LAYING PIPE |
| EA | UNDER GROUND |

| | | | | | | | | | |
|---|---|---|---|---|---|---|---|---|---|
| | | | | | | | | DESIGNED : | OLD TAG. |
| | | 5 | 10-01-22 | DST | FBI | | MODIF. DWG MDU 2022-PEP-003 | DRAWN : IFN : 28-11-2005 | |
| | | 4 | 30-07-20 | NAM | FBI | | MODIF. DWG. BASED ON MDU | CHECKED : | NEW TAG. |
| | | 3 | 26-11-14 | ALN | | | CHANGE FUNC. LOCATION | APPROVED : | |
| | | 2 | 08-04-14 | SBR | | | MODIF. DWG. BASED ON WO.8206977 | APPROVED : | |
| P&ID | HDF-12-3510-C (1 OF 4/REV.3) | 1 | 27-04-06 | SBR | | | MODIFICATION POINT NUMBER | FILE NAME : 8_HU_TO_CPA-1 | |
| DWG.No. | SUBJECT | No. | DATE | BY | CHK'D/SIGN. | | DESCRIPTION | | |
| REFERENCE DRAWINGS | | REVISIONS | | | | | | PERTAMINA HULU MAHAKAM | |

| | |
|---|---|
| M3 SOUTH GATHERING LINE | |
| 8_CPA_TO_HU (PIPELINE) | |
| (M3HU CLUSTER) | |
| SCALE NTS | DWG. No. |
| SHEET 5 1 OF 15 | REV. 5 |



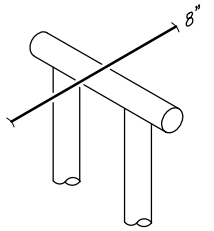
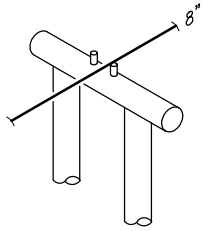
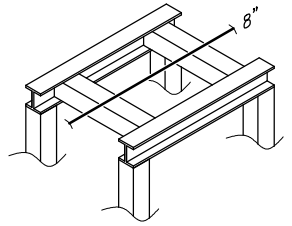
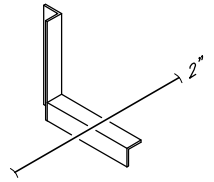




DETAIL OF SPLITE SLEEVED B




DETAIL OF SPLITE SLEEVED A

| No | SUPPORT DETAIL |
|---|---|
| A |  |
| B |  |
| H |  |
| I |  |

| CODE | DESCRIPTION |
|---|---|
| AA | NO SPACE FOR SCANNING |
| AC | BLOCKED BY EQUIPMENT |
| AD | BLOCKED BY SUPPORT (cannot be removed) |
| BA | HIGH LOCATION |
| BB | UNDER DECK |
| BC | LAYING PIPE |
| EA | UNDER GROUND |

| DWG.No. | SUBJECT |
|---|---|
| P&ID | HDF-12-3521-C (1 OF 4/REV.3) |

REFERENCE DRAWINGS

| No. | DATE | BY | CHK'D/SIGN. | DESCRIPTION |
|---|---|---|---|---|
| 5 | 10-01-22 | DST | FBI | MODIF. DWG MDU 2022-PEP-003 |
| 4 | 30-07-20 | NAM | FBI | MODIF. DWG. BASED ON MDU |
| 3 | 26-11-14 | ALN | | CHANGE FUNC. LOCATION |
| 2 | 08-04-14 | SBR | | MODIF. DWG. BASED ON WO.8206977 |
| 1 | 27-04-06 | SBR | | MODIFICATION POINT NUMBER |

REVISIONS

DESIGNED :
DRAWN : IFN : 28-11-2005
CHECKED :
APPROVED :
APPROVED :
FILE NAME : 8_HU_TO_CPA-2

PERTAMINA HULU MAHAKAM

OLD TAG.

NEW TAG.

M3 SOUTH GATHERING LINE

8_CPA_TO_HU
(PIPELINE)

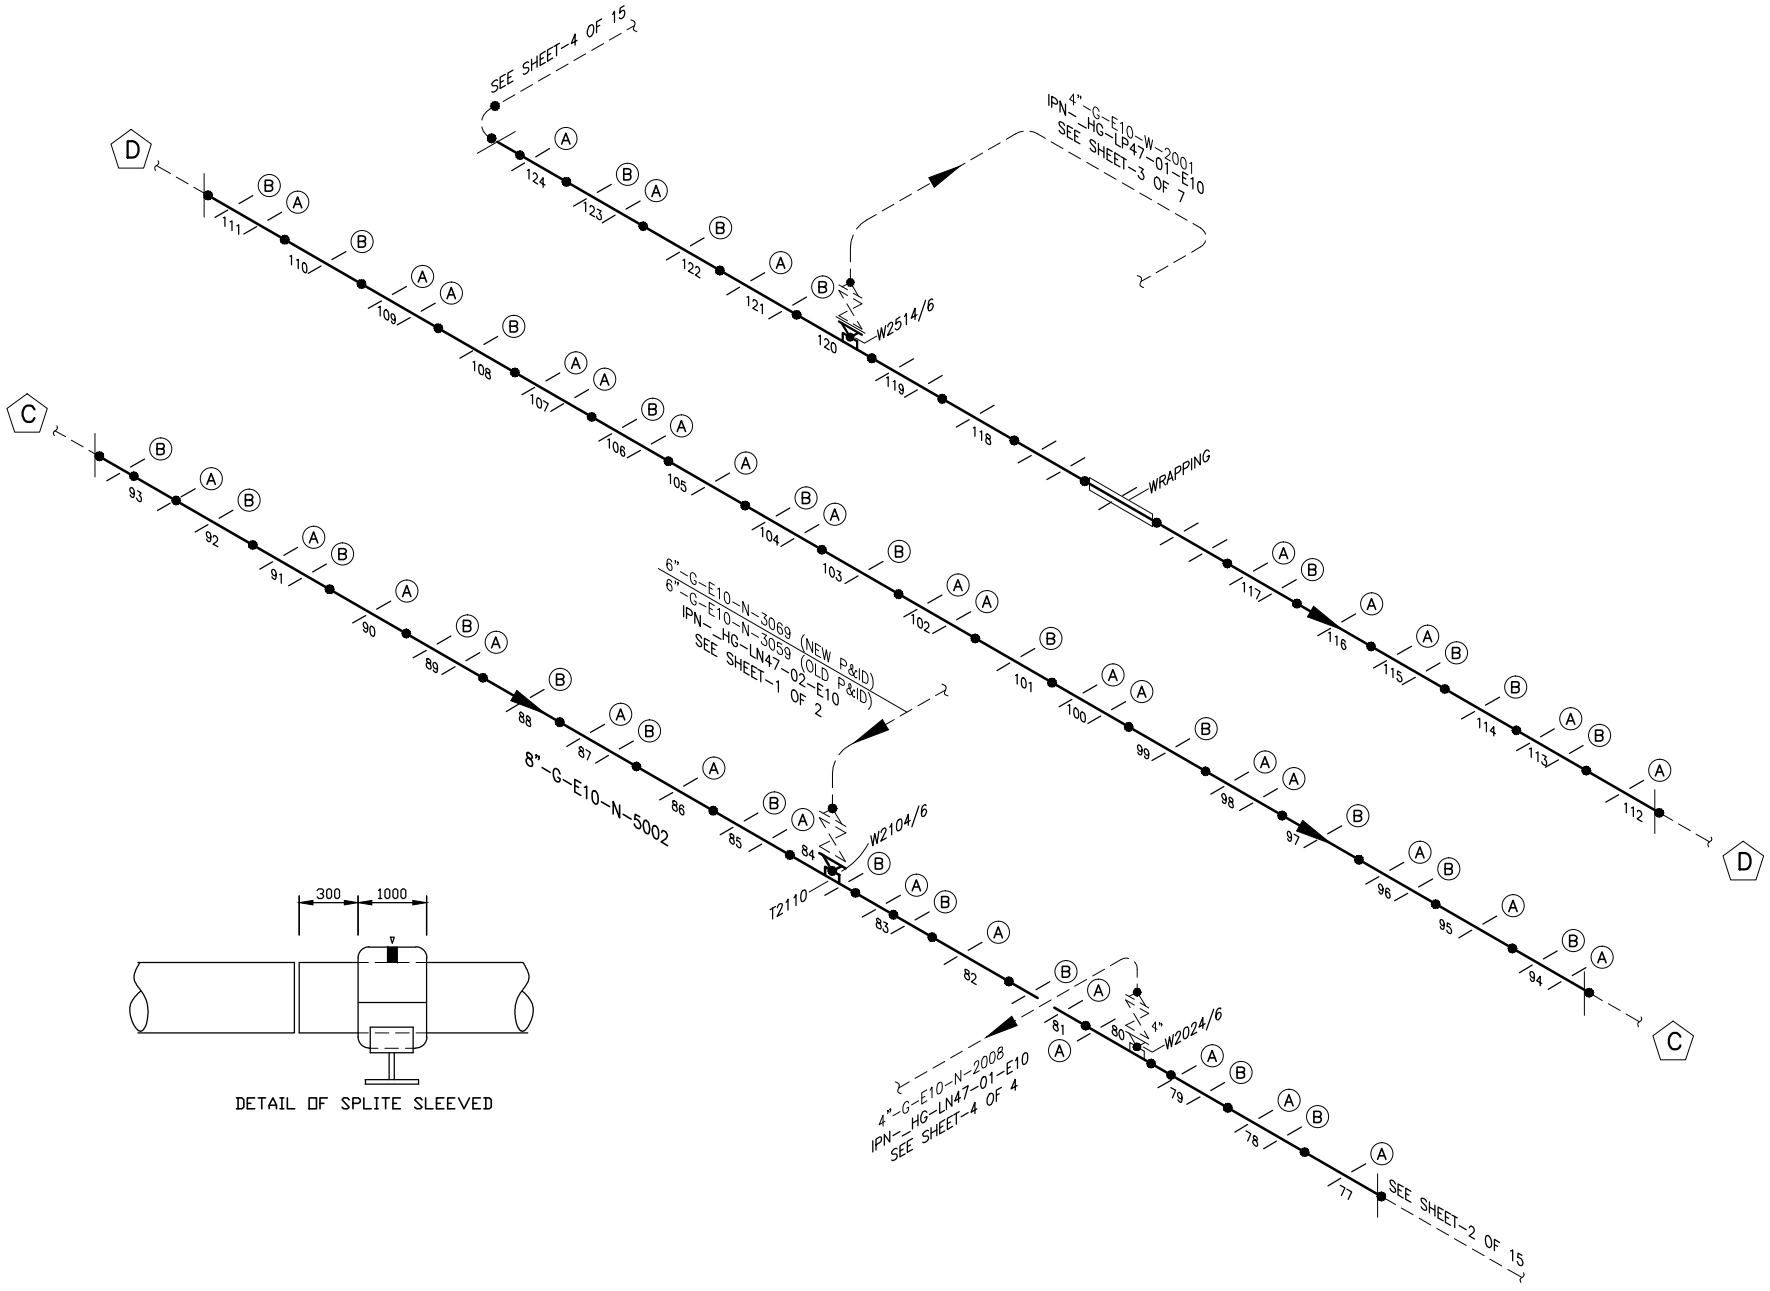
(M3HN CLUSTER)

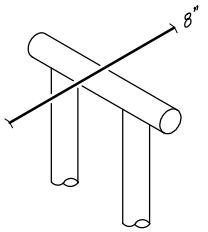
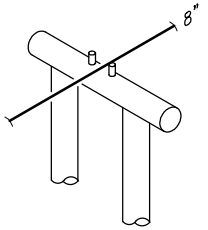
SCALE NTS

DWG. No.

SHEET 5
2 OF 15

REV. 5




| No | SUPPORT DETAIL |
|---|---|
| A |  |
| B |  |

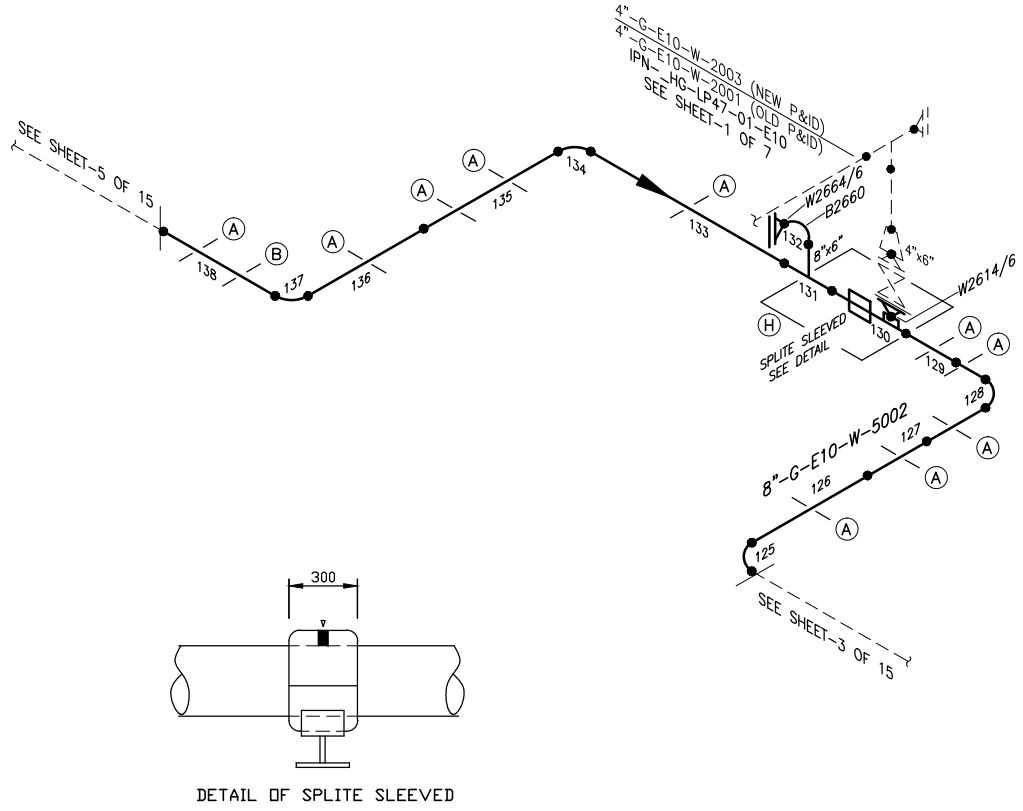
| CODE | DESCRIPTION |
|---|---|
| AA | NO SPACE FOR SCANNING |
| AC | BLOCKED BY EQUIPMENT |
| AD | BLOCKED BY SUPPORT (cannot be removed) |
| BA | HIGH LOCATION |
| BB | UNDER DECK |
| BC | LAYING PIPE |
| EA | UNDER GROUND |

| | | | | | | | | |
|---|---|---|---|---|---|---|---|---|
| | | 7 | 10-01-22 | DST | FBI | | MODIF. DWG MDU 2022-PEP-003 | DESIGNED : |
| | | 6 | 30-07-20 | NAM | FBI | | MODIF. DWG. BASED ON MDU | DRAWN : IFN : 28-11-2005 |
| | | 5 | 02-07-18 | DST | FBI | | RE-GROUPING BASED ON MARKUP P&ID | CHECKED : |
| P&ID | HDF-12-3530-C (1 OF 2/REV.3) | 4 | 26-11-14 | ALN | | | CHANGE FUNC. LOCATION | APPROVED : |
| P&ID | HDF-12-3523-C (1 OF 2/REV.4) | 3 | 08-04-14 | SBR | | | MODIF. DWG. BASED ON WO.8206977 | APPROVED : |
| P&ID | HDF-12-3522-C (1 OF 2/REV.4) | 2 | 01-05-09 | ALN | | | MOD. DWG BASED ON NOTIF. NO.14025980 | FILE NAME : 8_HU_TO_CPA-3 |
| DWG.No. | SUBJECT | No. | DATE | BY | CHK'D/SIGN. | | DESCRIPTION | |
| REFERENCE DRAWINGS | | REVISIONS | | | | | | |

| | |
|---|---|
| OLD TAG. | M3 SOUTH GATHERING LINE |
| NEW TAG. | 8_CPA_TO_HU (PIPELINE) |
| | (M3HN & M3HW CLUSTER) |

PERTAMINA HULU MAHAKAM

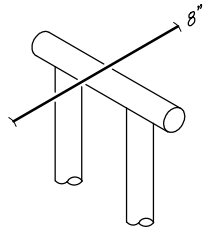
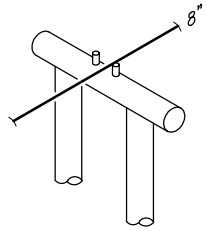
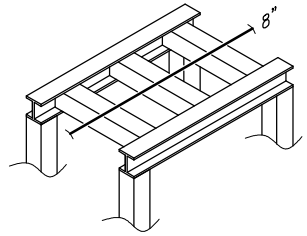
| SCALE | DWG. No. | SHEET | REV. |
|---|---|---|---|
| NTS | | 3 OF 15 | 7 |







DETAIL OF SPLITE SLEEVED

| No | SUPPORT DETAIL |
|---|---|
| A |  |
| B |  |
| H |  |

| CODE | DESCRIPTION |
|---|---|
| AA | NO SPACE FOR SCANNING |
| AC | BLOCKED BY EQUIPMENT |
| AD | BLOCKED BY SUPPORT (cannot be removed) |
| BA | HIGH LOCATION |
| BB | UNDER DECK |
| BC | LAYING PIPE |
| EA | UNDER GROUND |

| | | | | | | | | | |
|---|---|---|---|---|---|---|---|---|---|
| | | 7 | 10-01-22 | DST | FBI | | MODIF. DWG MDU 2022-PEP-003 | DESIGNED : | OLD TAG. |
| | | 6 | 30-07-20 | NAM | FBI | | MODIF. DWG. BASED ON MDU | DRAWN : IFN : 29-11-2005 | |
| | | 5 | 02-07-18 | DST | FBI | | RE-GROUPING BASED ON MARKUP P&ID | CHECKED : | NEW TAG. |
| | | 4 | 26-11-14 | ALN | | | CHANGE FUNC. LOCATION | APPROVED : | |
| | | 3 | 08-04-14 | SBR | | | MODIF. DWG. BASED ON WO.8206977 | APPROVED : | |
| P&ID | HDF-12-3531-C (1 OF 5/REV.3) | 2 | 01-05-09 | ALN | | | MOD. DWG BASED ON NOTIF. NO. 14025980 | FILE NAME : 8_HU_TO_CPA-4 | |
| DWG.No. | SUBJECT | No. | DATE | BY | CHK'D/SIGN. | | DESCRIPTION | PERTAMINA HULU MAHAKAM | SCALE NTS |
| REFERENCE DRAWINGS | | REVISIONS | | | | | | | DWG. No. |

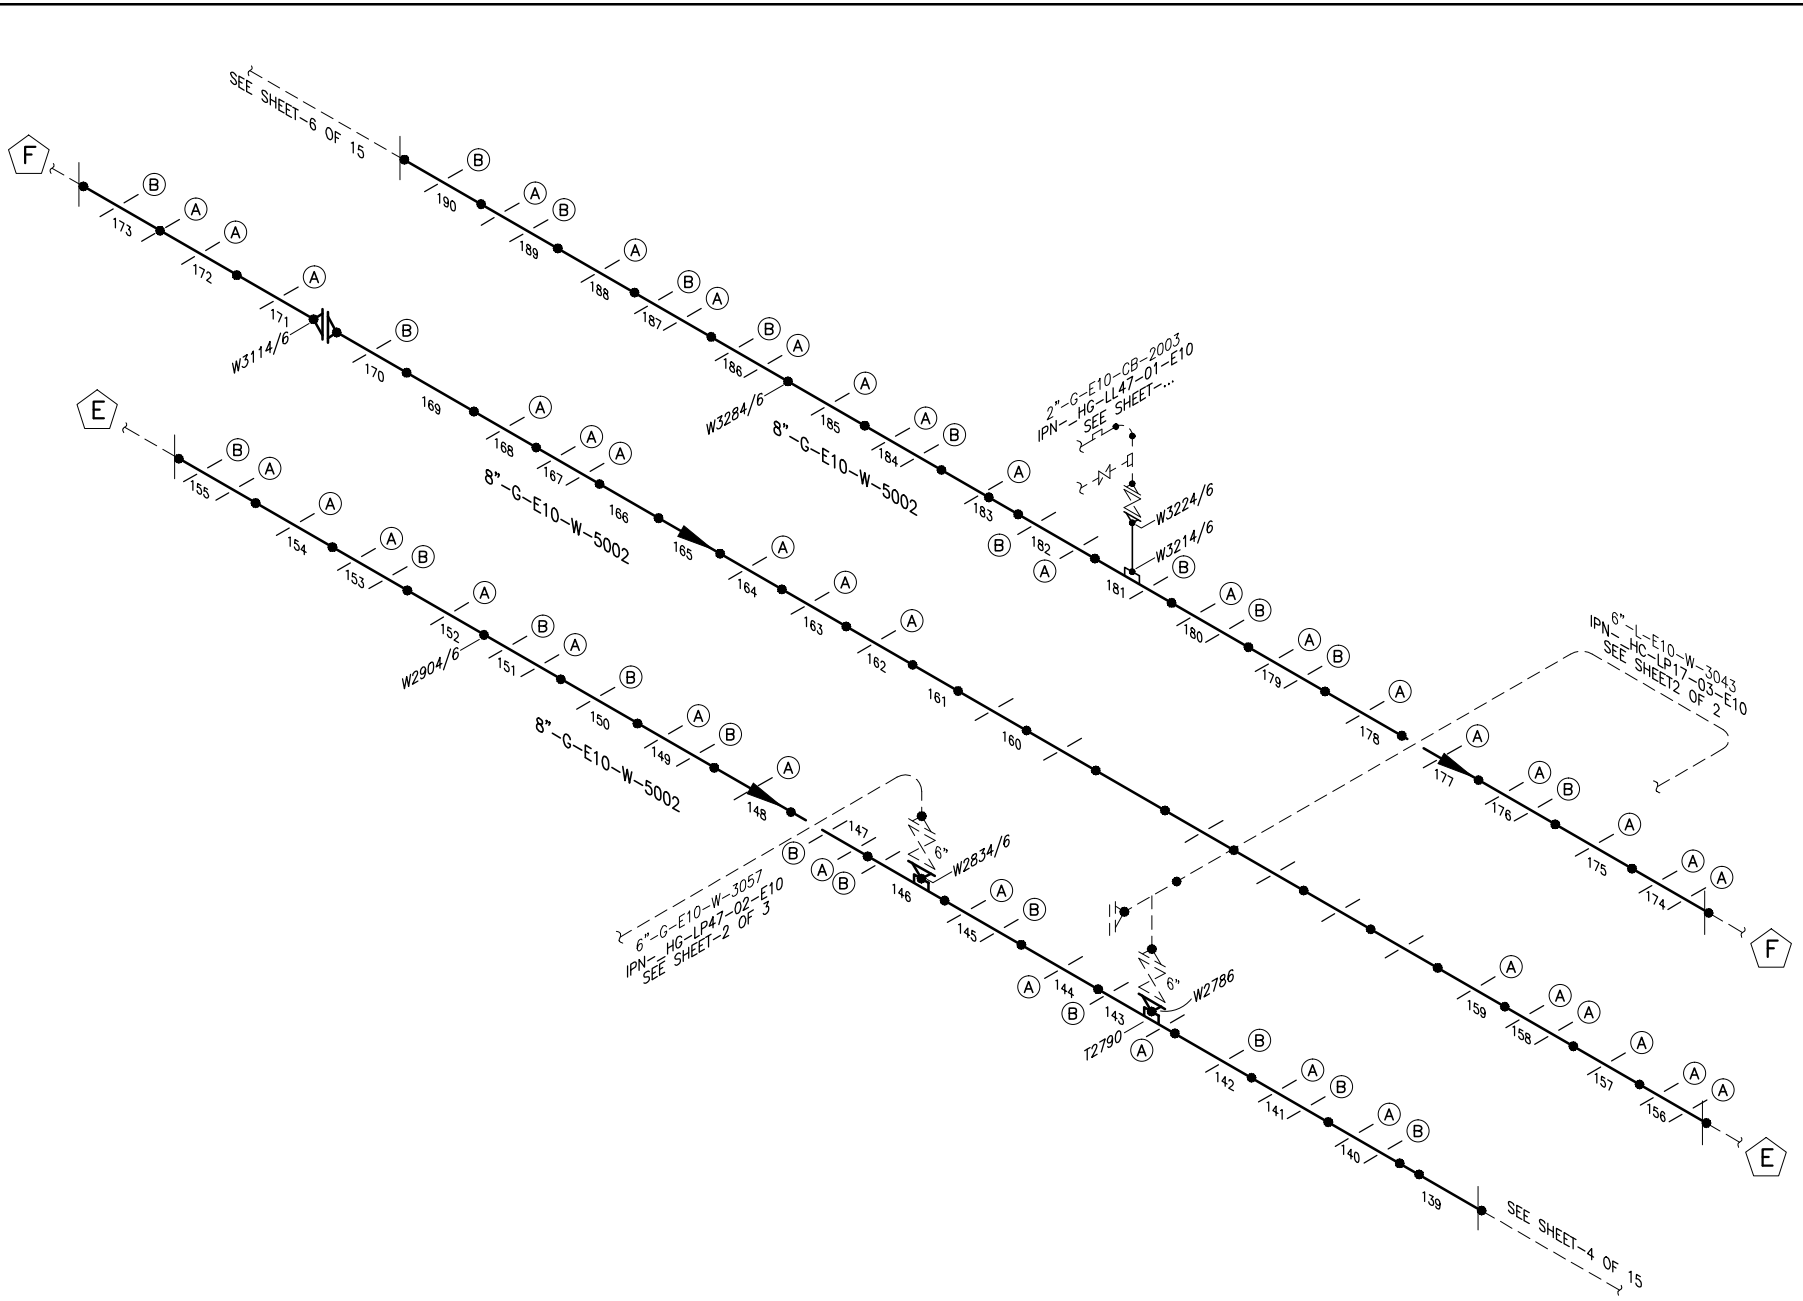
M3 SOUTH GATHERING LINE

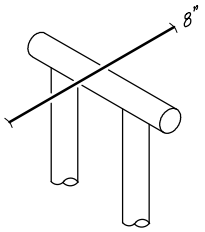
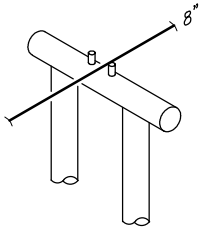
8_CPA_TO_HU
(PIPELINE)

(M3HW CLUSTER)

SHEET 4 OF 15

REV. 7




| No | SUPPORT DETAIL |
|---|---|
| A |  |
| B |  |

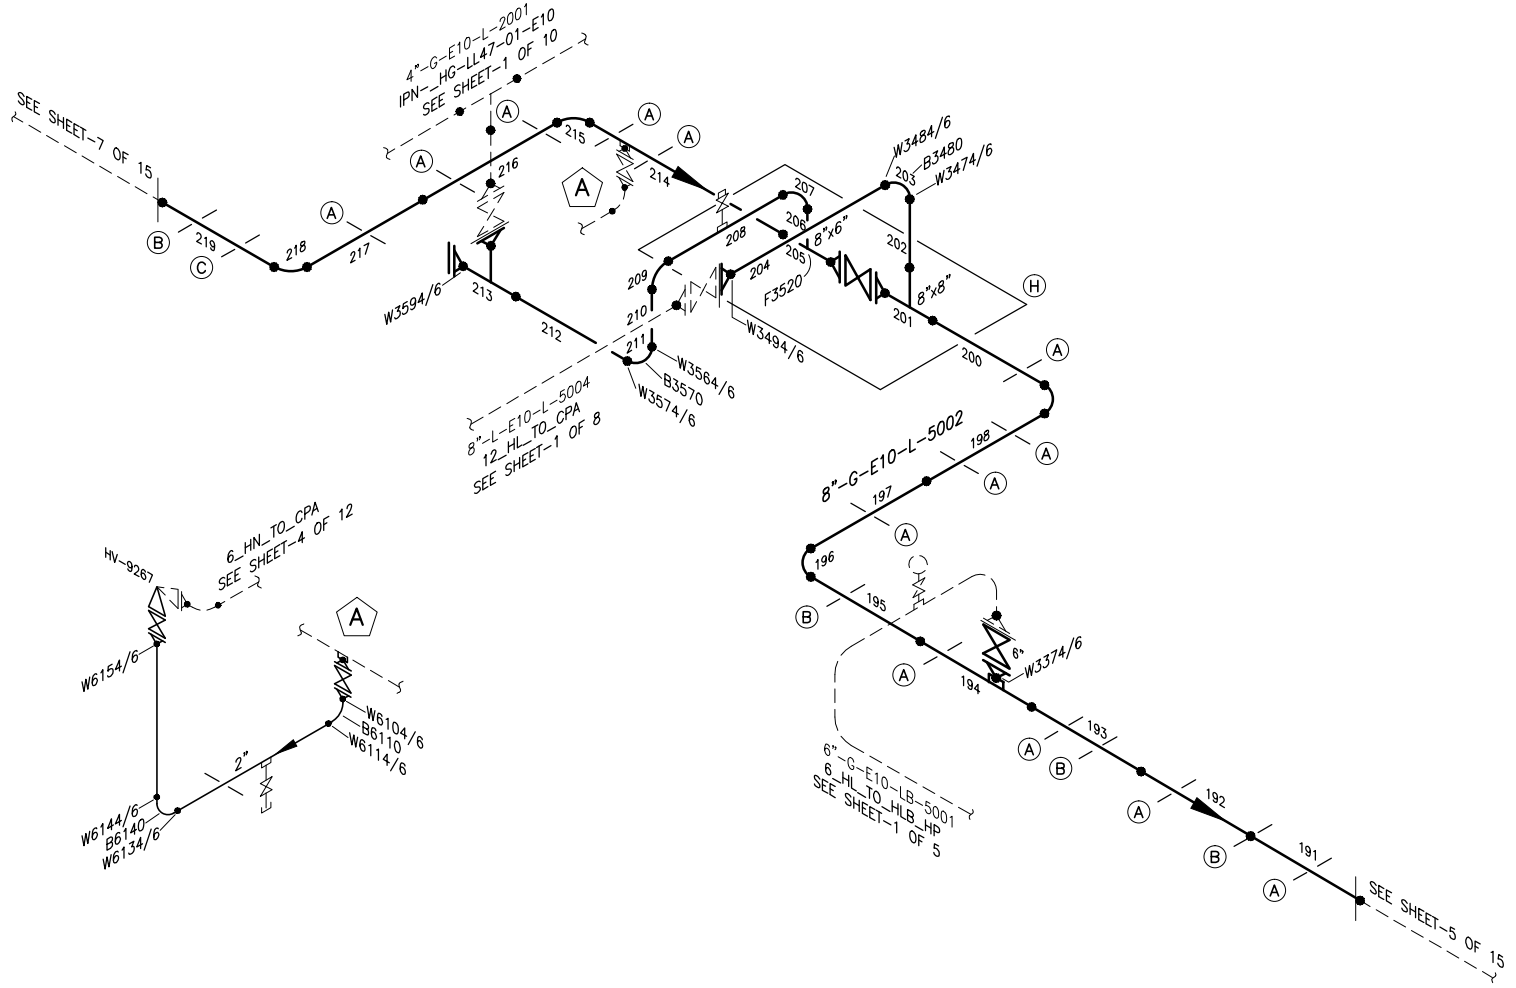
| CODE | DESCRIPTION |
|---|---|
| AA | NO SPACE FOR SCANNING |
| AC | BLOCKED BY EQUIPMENT |
| AD | BLOCKED BY SUPPORT (cannot be removed) |
| BA | HIGH LOCATION |
| BB | UNDER DECK |
| BC | LAYING PIPE |
| EA | UNDER GROUND |

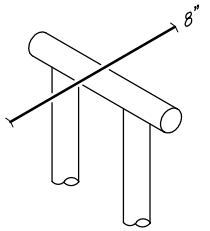
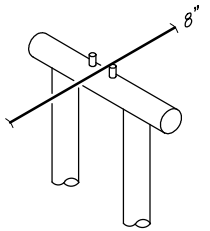
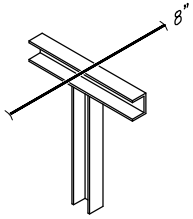
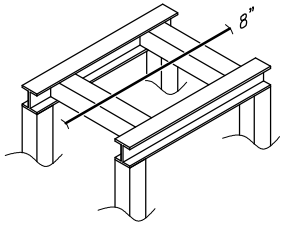
| | | | | | | | | |
|---|---|---|---|---|---|---|---|---|
| | | 7 | 10-01-22 | DST | FBI | | MODIF. DWG MDU 2022-PEP-003 | DESIGNED : |
| | | 6 | 30-07-20 | NAM | FBI | | MODIF. DWG. BASED ON MDU | DRAWN : IFN : 29-11-2005 |
| | | 5 | 02-07-18 | DST | FBI | | RE-GROUPING BASED ON MARKUP P&ID | CHECKED : |
| P&ID | HDF-12-3550-C (1 OF 4/REV.4) | 4 | 26-11-14 | ALN | | | CHANGE FUNC. LOCATION | APPROVED : |
| P&ID | HDF-12-3533-C (1 OF 3/REV.4) | 3 | 08-04-14 | SBR | | | MODIF. DWG. BASED ON WO.8206977 | APPROVED : |
| P&ID | HDF-12-3532-C (1 OF 3/REV.5) | 2 | 01-05-09 | ALN | | | MOD. DWG BASED ON NOTIF. NO. 14025980 | FILE NAME : 8_HU_TO_CPA-5 |
| DWG.No. | SUBJECT | No. | DATE | BY | CHK'D/SIGN. | | DESCRIPTION | |
| REFERENCE DRAWINGS | | REVISIONS | | | | | | |

PERTAMINA HULU MAHAKAM

| | |
|---|---|
| OLD TAG. | M3 SOUTH GATHERING LINE |
| NEW TAG. | 8_CPA_TO_HU (PIPELINE) |
| | (M3HW & M3HL CLUSTER) |

| SCALE | DWG. No. | SHEET | REV. |
|---|---|---|---|
| NTS | | 5 OF 15 | 7 |




| No | SUPPORT DETAIL |
|---|---|
| A |  |
| B |  |
| C |  |
| H |  |

| CODE | DESCRIPTION |
|---|---|
| AA | NO SPACE FOR SCANNING |
| AC | BLOCKED BY EQUIPMENT |
| AD | BLOCKED BY SUPPORT (cannot be removed) |
| BA | HIGH LOCATION |
| BB | UNDER DECK |
| BC | LAYING PIPE |
| EA | UNDER GROUND |

| DWG.No. | SUBJECT |
|---|---|
| P&ID | HDF-12-3550-C (1 OF 4/REV.4) |
| P&ID | HDF-12-3551-C (1 OF 4/REV.3) |

REFERENCE DRAWINGS

| No. | DATE | BY | CHK'D/SIGN. | DESCRIPTION |
|---|---|---|---|---|
| 6 | 10-01-22 | DST | FBI | MODIF. DWG MDU 2022-PEP-003 |
| 5 | 30-07-20 | NAM | FBI | MODIF. DWG. BASED ON MDU |
| 4 | 02-07-18 | DST | FBI | RE-GROUPING BASED ON MARKUP P&ID |
| 3 | 26-11-14 | ALN | | CHANGE FUNC. LOCATION |
| 2 | 08-04-14 | SBR | | MODIF. DWG. BASED ON WO.8206977 |
| 1 | 27-04-06 | SBR | | MODIFICATION POINT NUMBER |

REVISIONS

DESIGNED :
DRAWN : IFN : 29-11-2005
CHECKED :
APPROVED :
APPROVED :
FILE NAME : 8_HU_TO_CPA-6

PERTAMINA HULU MAHAKAM

OLD TAG.

NEW TAG.

M3 SOUTH GATHERING LINE

8_CPA_TO_HU
(PIPELINE)

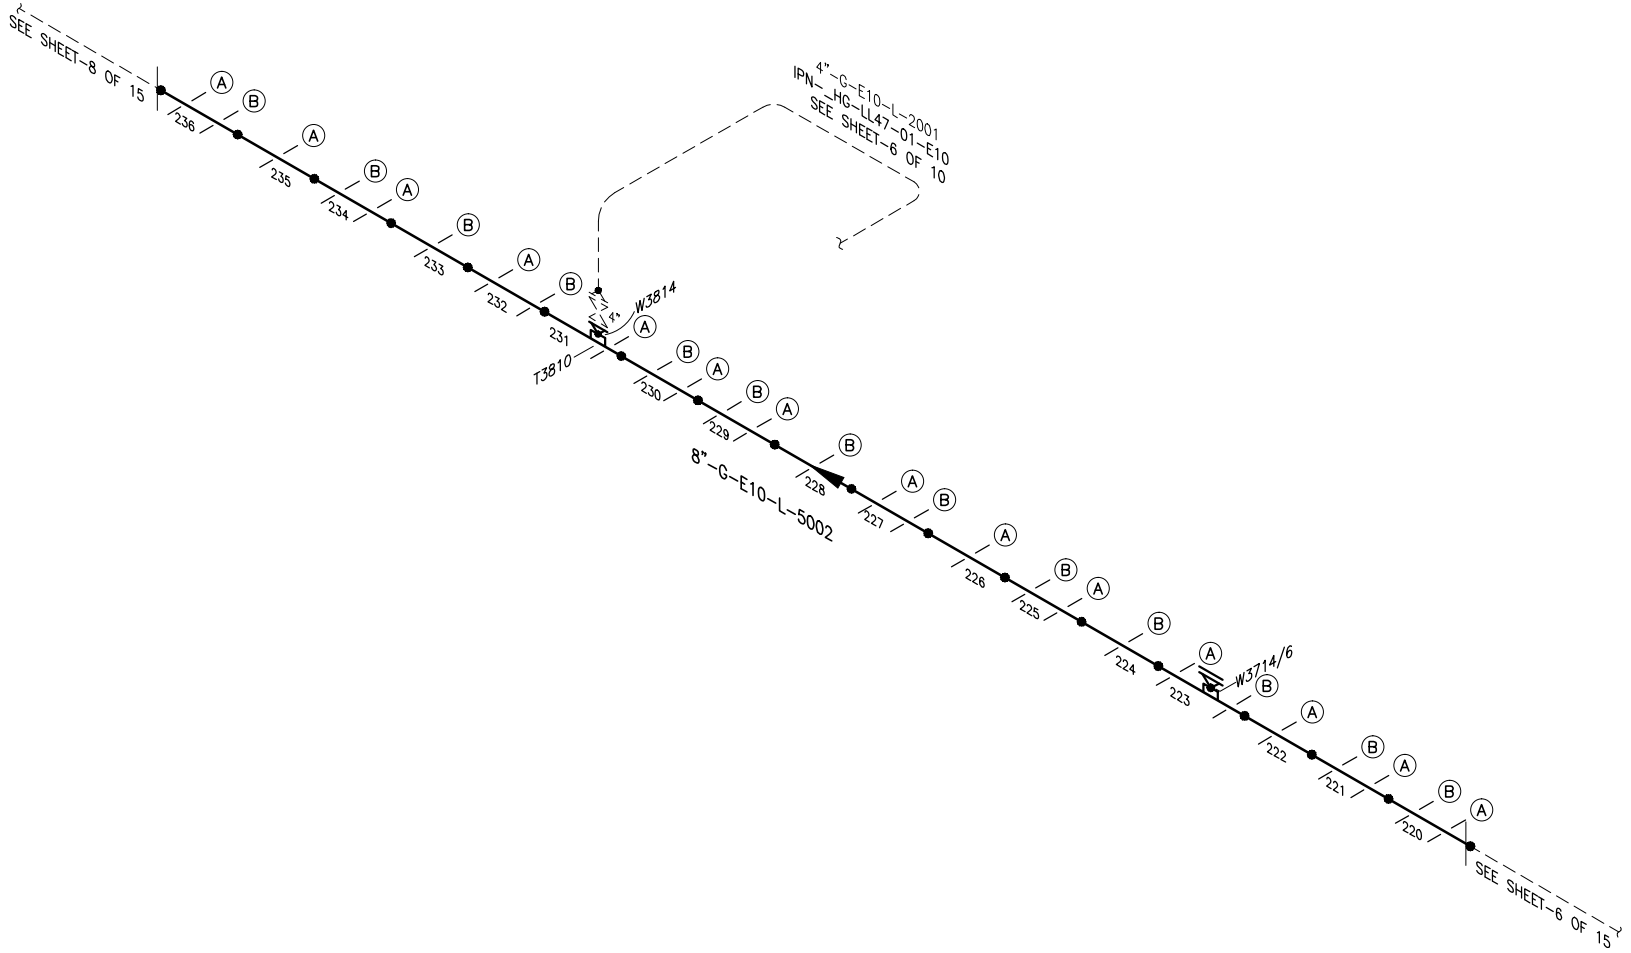
(M3HL CLUSTER)

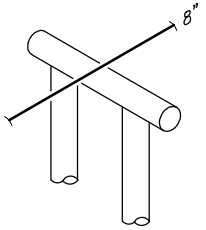
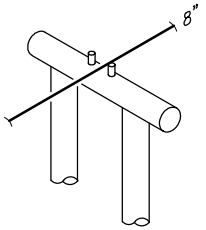
SCALE NTS

DWG. No.

SHEET 6
6 OF 15

REV. 6




| No | SUPPORT DETAIL |
|---|---|
| A |  |
| B |  |

| CODE | DESCRIPTION |
|---|---|
| AA | NO SPACE FOR SCANNING |
| AC | BLOCKED BY EQUIPMENT |
| AD | BLOCKED BY SUPPORT (cannot be removed) |
| BA | HIGH LOCATION |
| BB | UNDER DECK |
| BC | LAYING PIPE |
| EA | UNDER GROUND |

| DWG.No. | SUBJECT |
|---|---|
| P&ID | HDF-12-3553-C (1 OF 5/REV.3) |
| P&ID | HDF-12-3552-C (1 OF 5/REV.3) |

REFERENCE DRAWINGS

| No. | DATE | BY | CHK'D/SIGN. | DESCRIPTION |
|---|---|---|---|---|
| 6 | 10-01-22 | DST | FBI | MODIF. DWG MDU 2022-PEP-003 |
| 5 | 30-07-20 | NAM | FBI | MODIF. DWG. BASED ON MDU |
| 4 | 02-07-18 | DST | FBI | RE-GROUPING BASED ON MARKUP P&ID |
| 3 | 26-11-14 | ALN | | CHANGE FUNC. LOCATION |
| 2 | 08-04-14 | SBR | | MODIF. DWG. BASED ON WO.8206977 |
| 1 | 27-04-06 | SBR | | MODIFICATION POINT NUMBER |

REVISIONS

DESIGNED :
DRAWN : IFN : 30-11-2005
CHECKED :
APPROVED :
APPROVED :
FILE NAME : 8_HU_TO_CPA-7

PERTAMINA HULU MAHAKAM

OLD TAG.

NEW TAG.

M3 SOUTH GATHERING LINE

8_CPA_TO_HU
(PIPELINE)

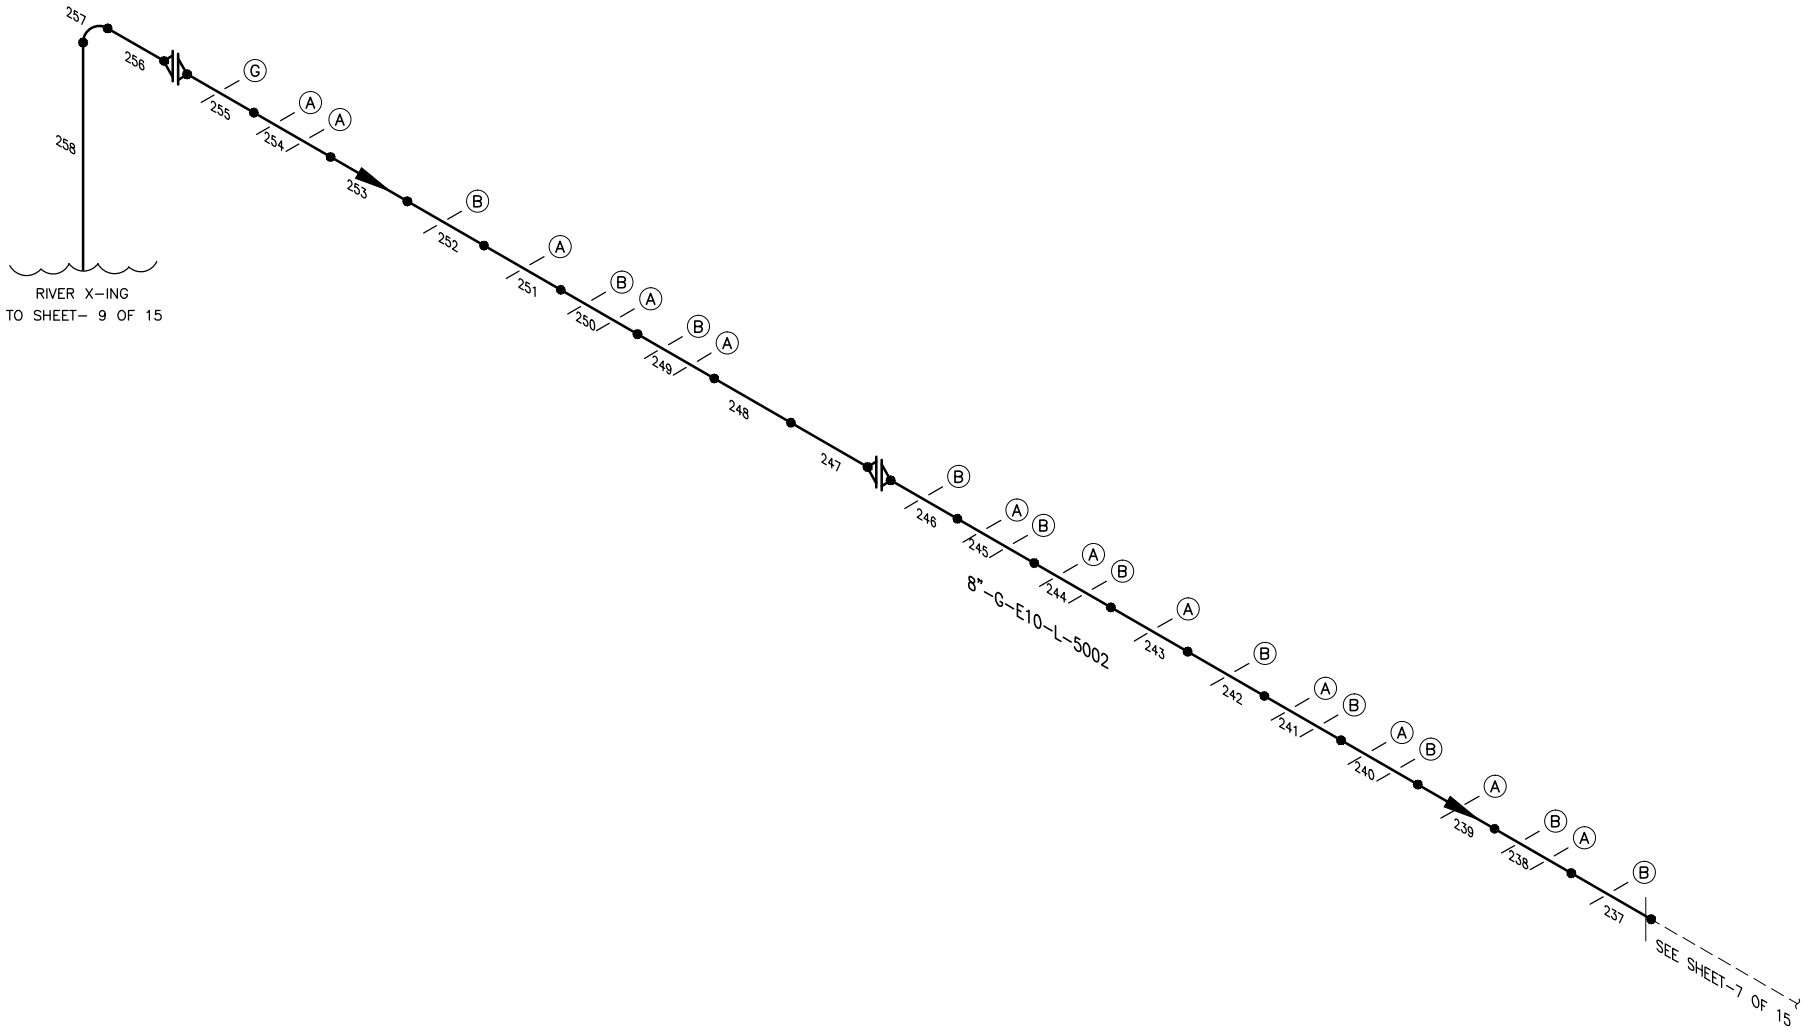
(M3HL CLUSTER)

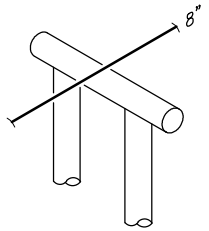
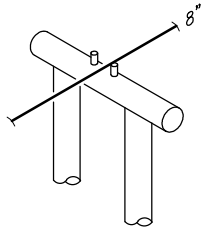
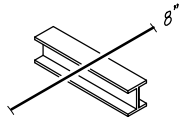
SCALE NTS

DWG. No.

SHEET 6
7 OF 15

REV. 6




| No | SUPPORT DETAIL |
|---|---|
| A |  |
| B |  |
| G |  |

| CODE | DESCRIPTION |
|---|---|
| AA | NO SPACE FOR SCANNING |
| AC | BLOCKED BY EQUIPMENT |
| AD | BLOCKED BY SUPPORT (cannot be removed) |
| BA | HIGH LOCATION |
| BB | UNDER DECK |
| BC | LAYING PIPE |
| EA | UNDER GROUND |

| | | | | | | | | | |
|---|---|---|---|---|---|---|---|---|---|
| | | | | | | | | DESIGNED : | OLD TAG. |
| | | 5 | 10-01-22 | DST | FBI | | MODIF. DWG MDU 2022-PEP-003 | DRAWN : IFN : 30-11-2005 | |
| | | 4 | 30-07-20 | NAM | FBI | | MODIF. DWG. BASED ON MDU | CHECKED : | NEW TAG. |
| | | 3 | 26-11-14 | ALN | | | CHANGE FUNC. LOCATION | APPROVED : | |
| | | 2 | 08-04-14 | SBR | | | MODIF. DWG. BASED ON WO.8206977 | APPROVED : | |
| P&ID | HDF-12-3555-C (1 OF 1/REV.2) | 1 | 27-04-06 | SBR | | | MODIFICATION POINT NUMBER | FILE NAME : 8_HU_TO_CPA-8 | |
| DWG.No. | SUBJECT | No. | DATE | BY | CHK'D/SIGN. | | DESCRIPTION | PERTAMINA HULU MAHAKAM | SCALE NTS |
| REFERENCE DRAWINGS | | REVISIONS | | | | | | | DWG. No. |

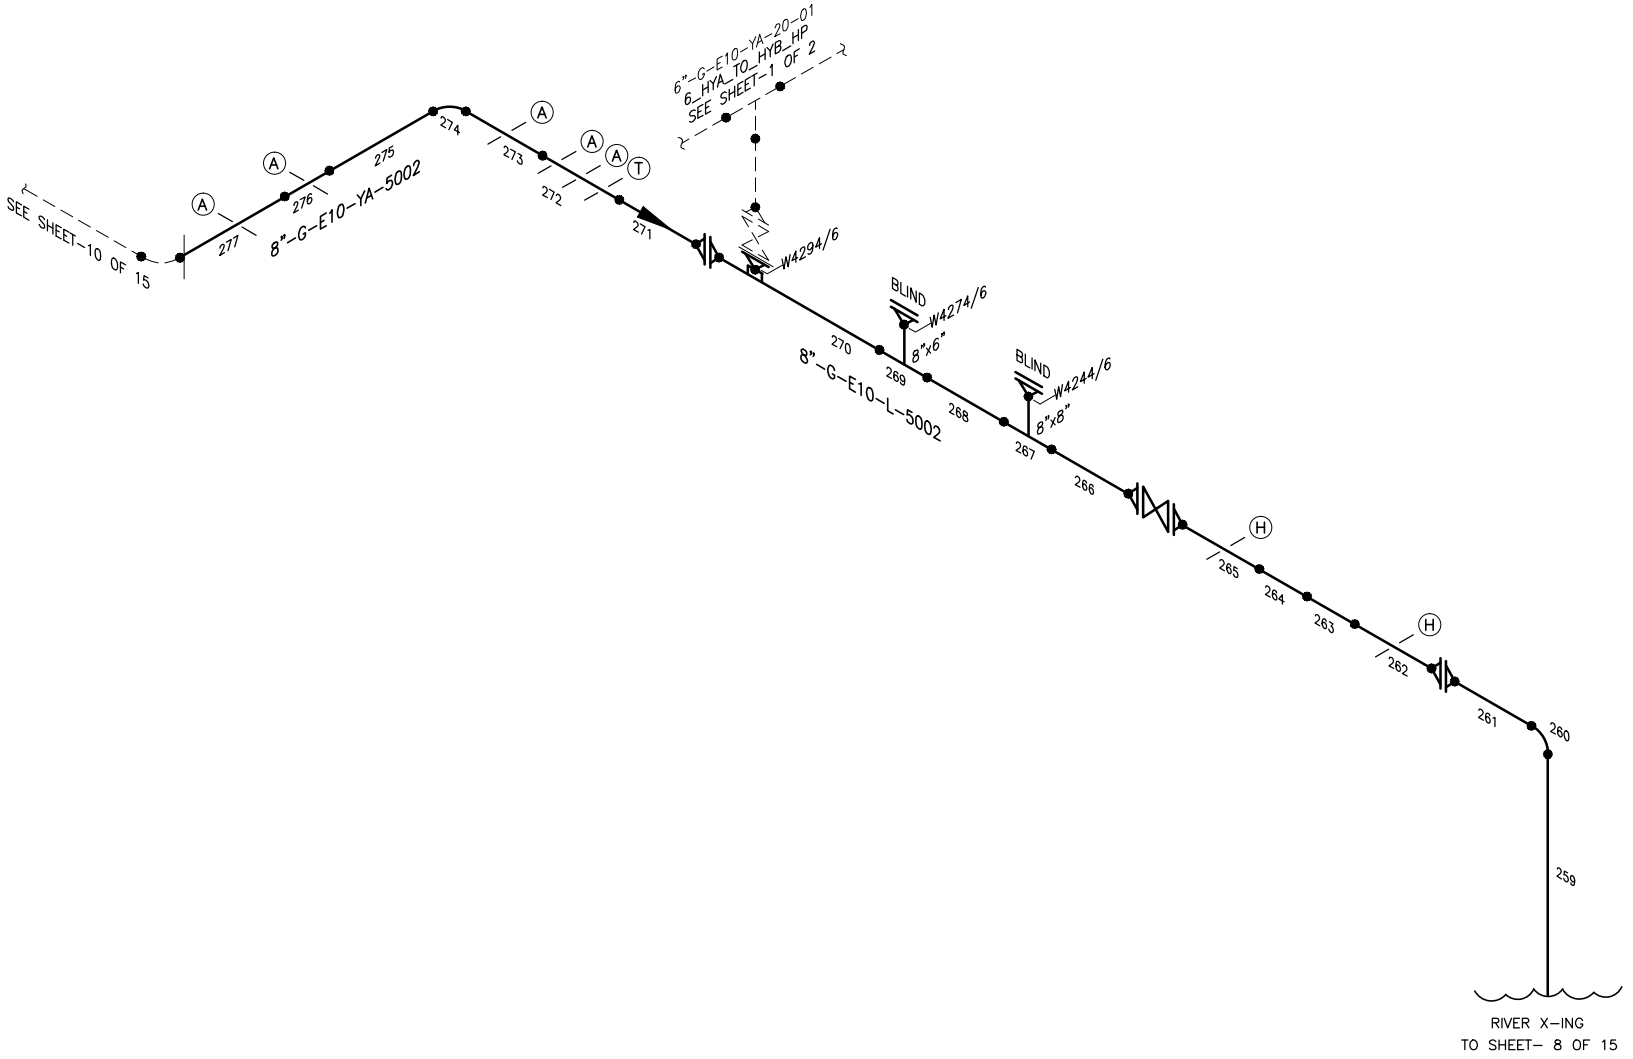
M3 SOUTH GATHERING LINE

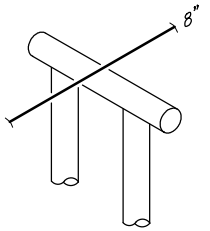
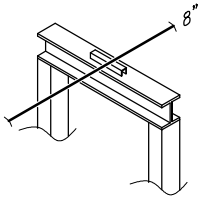
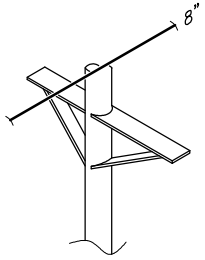
8_CPA_TO_HU
(PIPELINE)

(M3HYA CLUSTER)

SHEET 5
8 OF 15

REV. 5




| No | SUPPORT DETAIL |
|---|---|
| A |  |
| H |  |
| T |  |

| CODE | DESCRIPTION |
|---|---|
| AA | NO SPACE FOR SCANNING |
| AC | BLOCKED BY EQUIPMENT |
| AD | BLOCKED BY SUPPORT (cannot be removed) |
| BA | HIGH LOCATION |
| BB | UNDER DECK |
| BC | LAYING PIPE |
| EA | UNDER GROUND |

| | | No. | DATE | BY | CHK'D/SIGN. | DESCRIPTION |
|---|---|---|---|---|---|---|
| | | 6 | 10-01-22 | DST | FBI | MODIF. DWG MDU 2022-PEP-003 |
| | | 5 | 30-07-20 | NAM | FBI | MODIF. DWG. BASED ON MDU |
| | | 4 | 02-07-18 | DST | FBI | RE-GROUPING BASED ON MARKUP P&ID |
| | | 3 | 26-11-14 | ALN | | CHANGE FUNC. LOCATION |
| | | 2 | 08-04-14 | SBR | | MODIF. DWG. BASED ON WO.8206977 |
| P&ID | HDF-12-3555-C (1 OF 1/REV.2) | 1 | 27-04-06 | SBR | | MODIFICATION POINT NUMBER |
| DWG.No. | SUBJECT | | | | | |

REFERENCE DRAWINGS

REVISIONS

DESIGNED :
DRAWN : IFN : 30-11-2005
CHECKED :
APPROVED :
APPROVED :
FILE NAME : 8_HU_TO_CPA-9

PERTAMINA HULU MAHAKAM

OLD TAG.

NEW TAG.

M3 SOUTH GATHERING LINE

8_CPA_TO_HU
(PIPELINE)

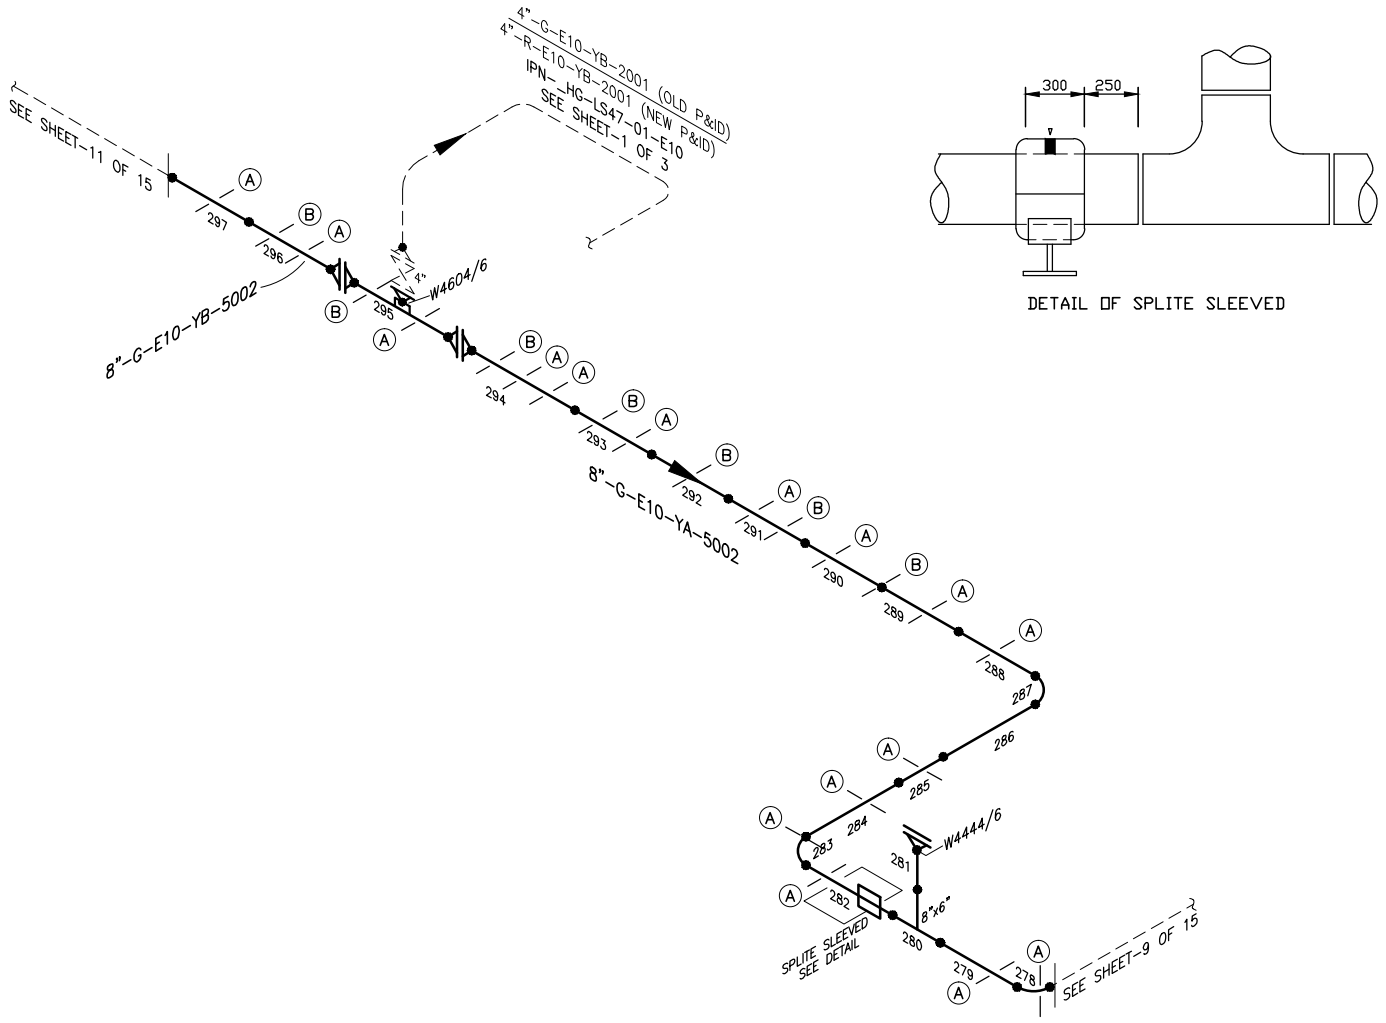
(M3HYA CLUSTER)

SCALE NTS

DWG. No.

SHEET 6
9 OF 15

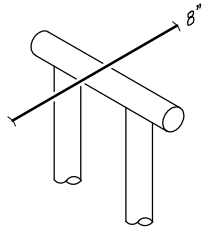
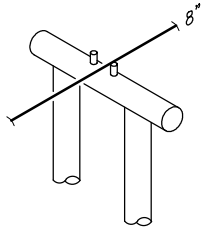
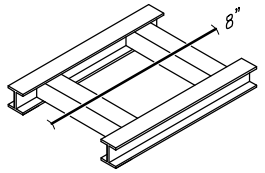
REV. 6







DETAIL OF SPLITE SLEEVED

| No | SUPPORT DETAIL |
|---|---|
| A |  |
| B |  |
| H |  |

| CODE | DESCRIPTION |
|---|---|
| AA | NO SPACE FOR SCANNING |
| AC | BLOCKED BY EQUIPMENT |
| AD | BLOCKED BY SUPPORT (cannot be removed) |
| BA | HIGH LOCATION |
| BB | UNDER DECK |
| BC | LAYING PIPE |
| EA | UNDER GROUND |

| DWG.No. | SUBJECT |
|---|---|
| P&ID | HDF-12-3555-C (1 OF 1/REV.2) |
| P&ID | HDF-12-3570-C (1 OF 4/REV.3) |

REFERENCE DRAWINGS

| No. | DATE | BY | CHK'D/SIGN. | DESCRIPTION |
|---|---|---|---|---|
| 5 | 10-01-22 | DST | FBI | MODIF. DWG MDU 2022-PEP-003 |
| 4 | 30-07-20 | NAM | FBI | MODIF. DWG. BASED ON MDU |
| 3 | 26-11-14 | ALN | | CHANGE FUNC. LOCATION |
| 2 | 08-04-14 | SBR | | MODIF. DWG. BASED ON WO.8206977 |
| 1 | 27-04-06 | SBR | | MODIFICATION POINT NUMBER |

REVISIONS

DESIGNED :
DRAWN : IFN : 30-11-2005
CHECKED :
APPROVED :
APPROVED :
FILE NAME : 8_HU_TO_CPA-10

PERTAMINA HULU MAHAKAM

OLD TAG.

NEW TAG.

M3 SOUTH GATHERING LINE

8_CPA_TO_HU
(PIPELINE)

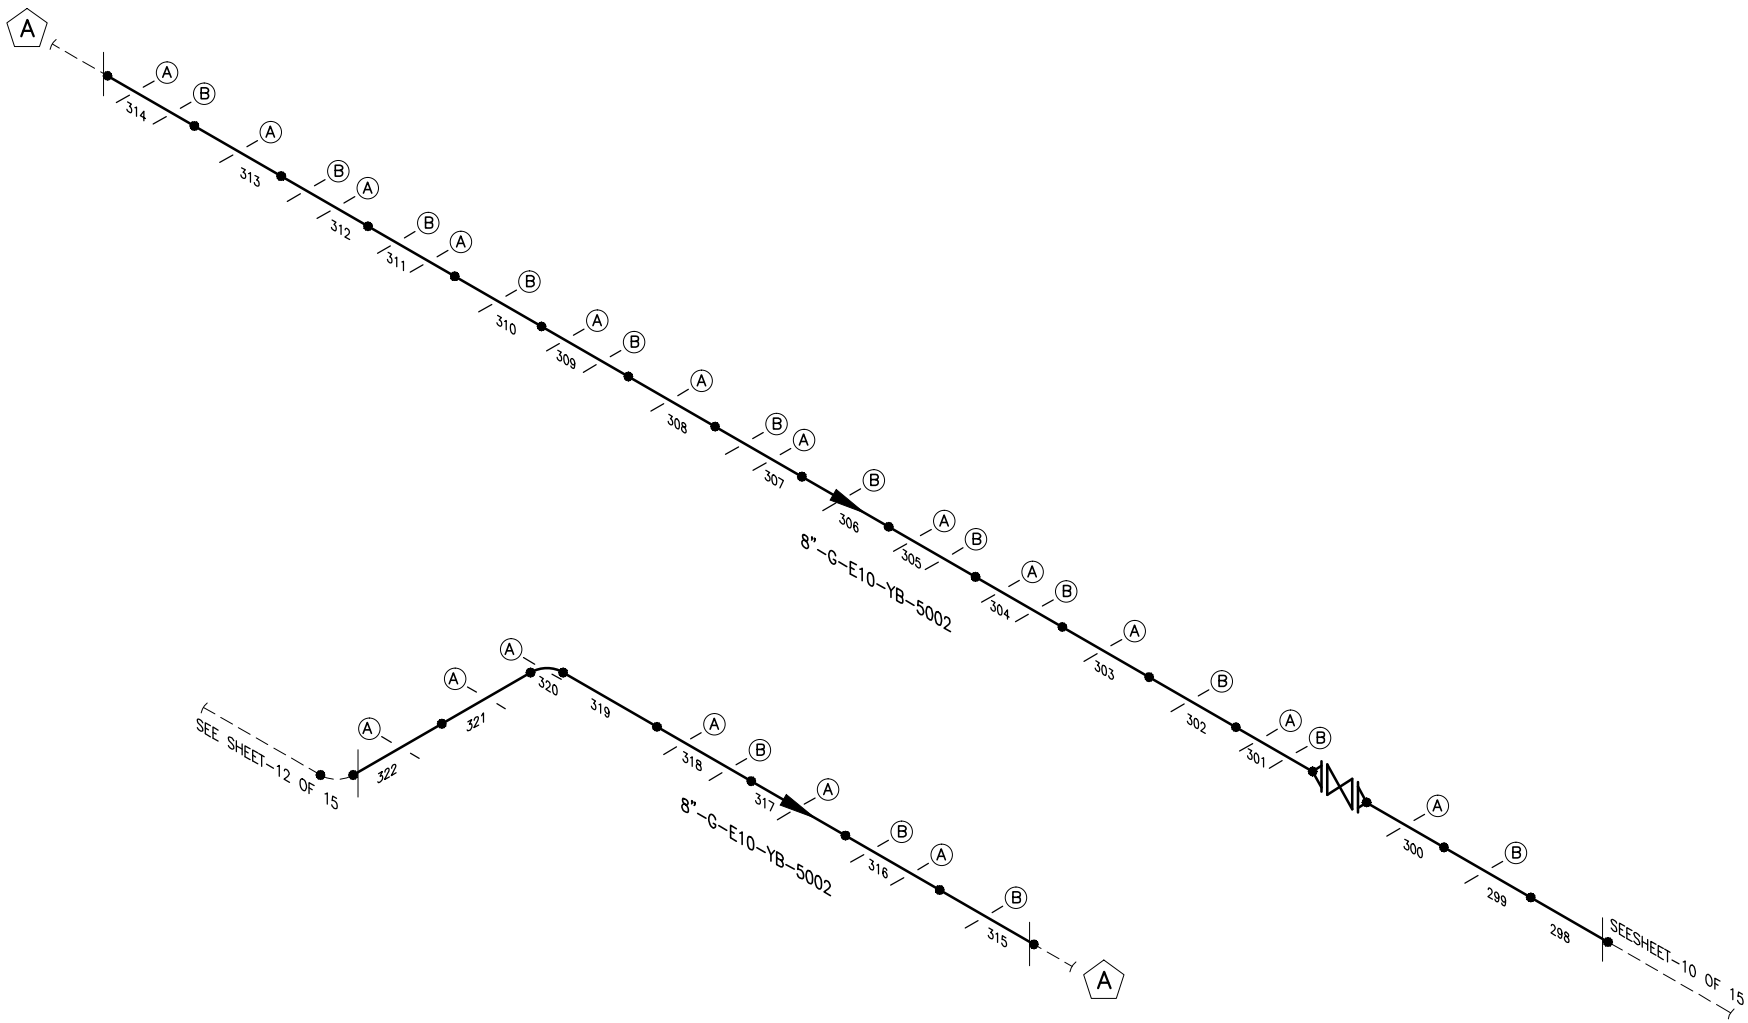
(M3HYA & M3HYB CLUSTER)

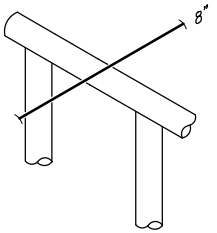
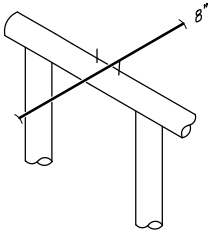
SCALE NTS

DWG. No.

SHEET 5 10 OF 15

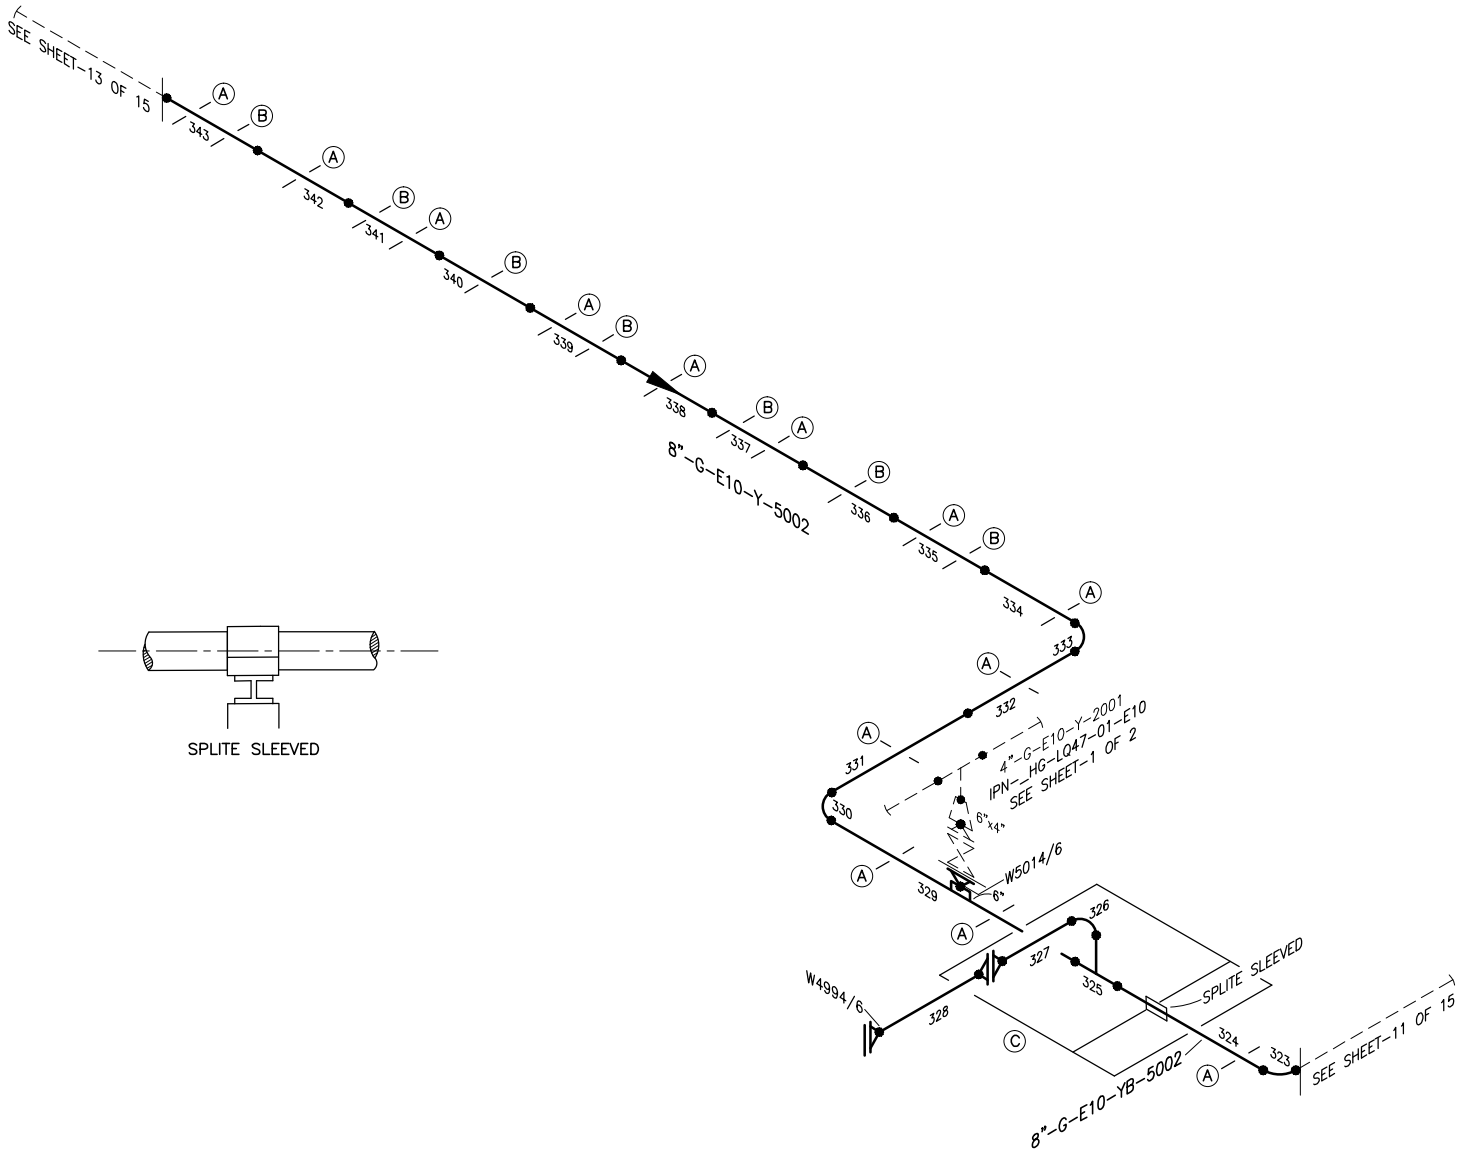
REV. 5

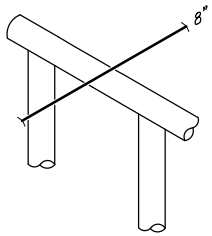
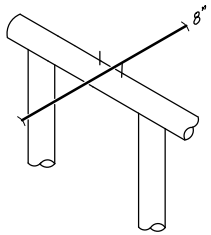
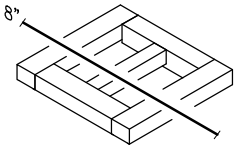



| No | SUPPORT DETAIL |
|---|---|
| A |  |
| B |  |

| CODE | DESCRIPTION |
|---|---|
| AA | NO SPACE FOR SCANNING |
| AC | BLOCKED BY EQUIPMENT |
| AD | BLOCKED BY SUPPORT (cannot be removed) |
| BA | HIGH LOCATION |
| BB | UNDER DECK |
| BC | LAYING PIPE |
| EA | UNDER GROUND |

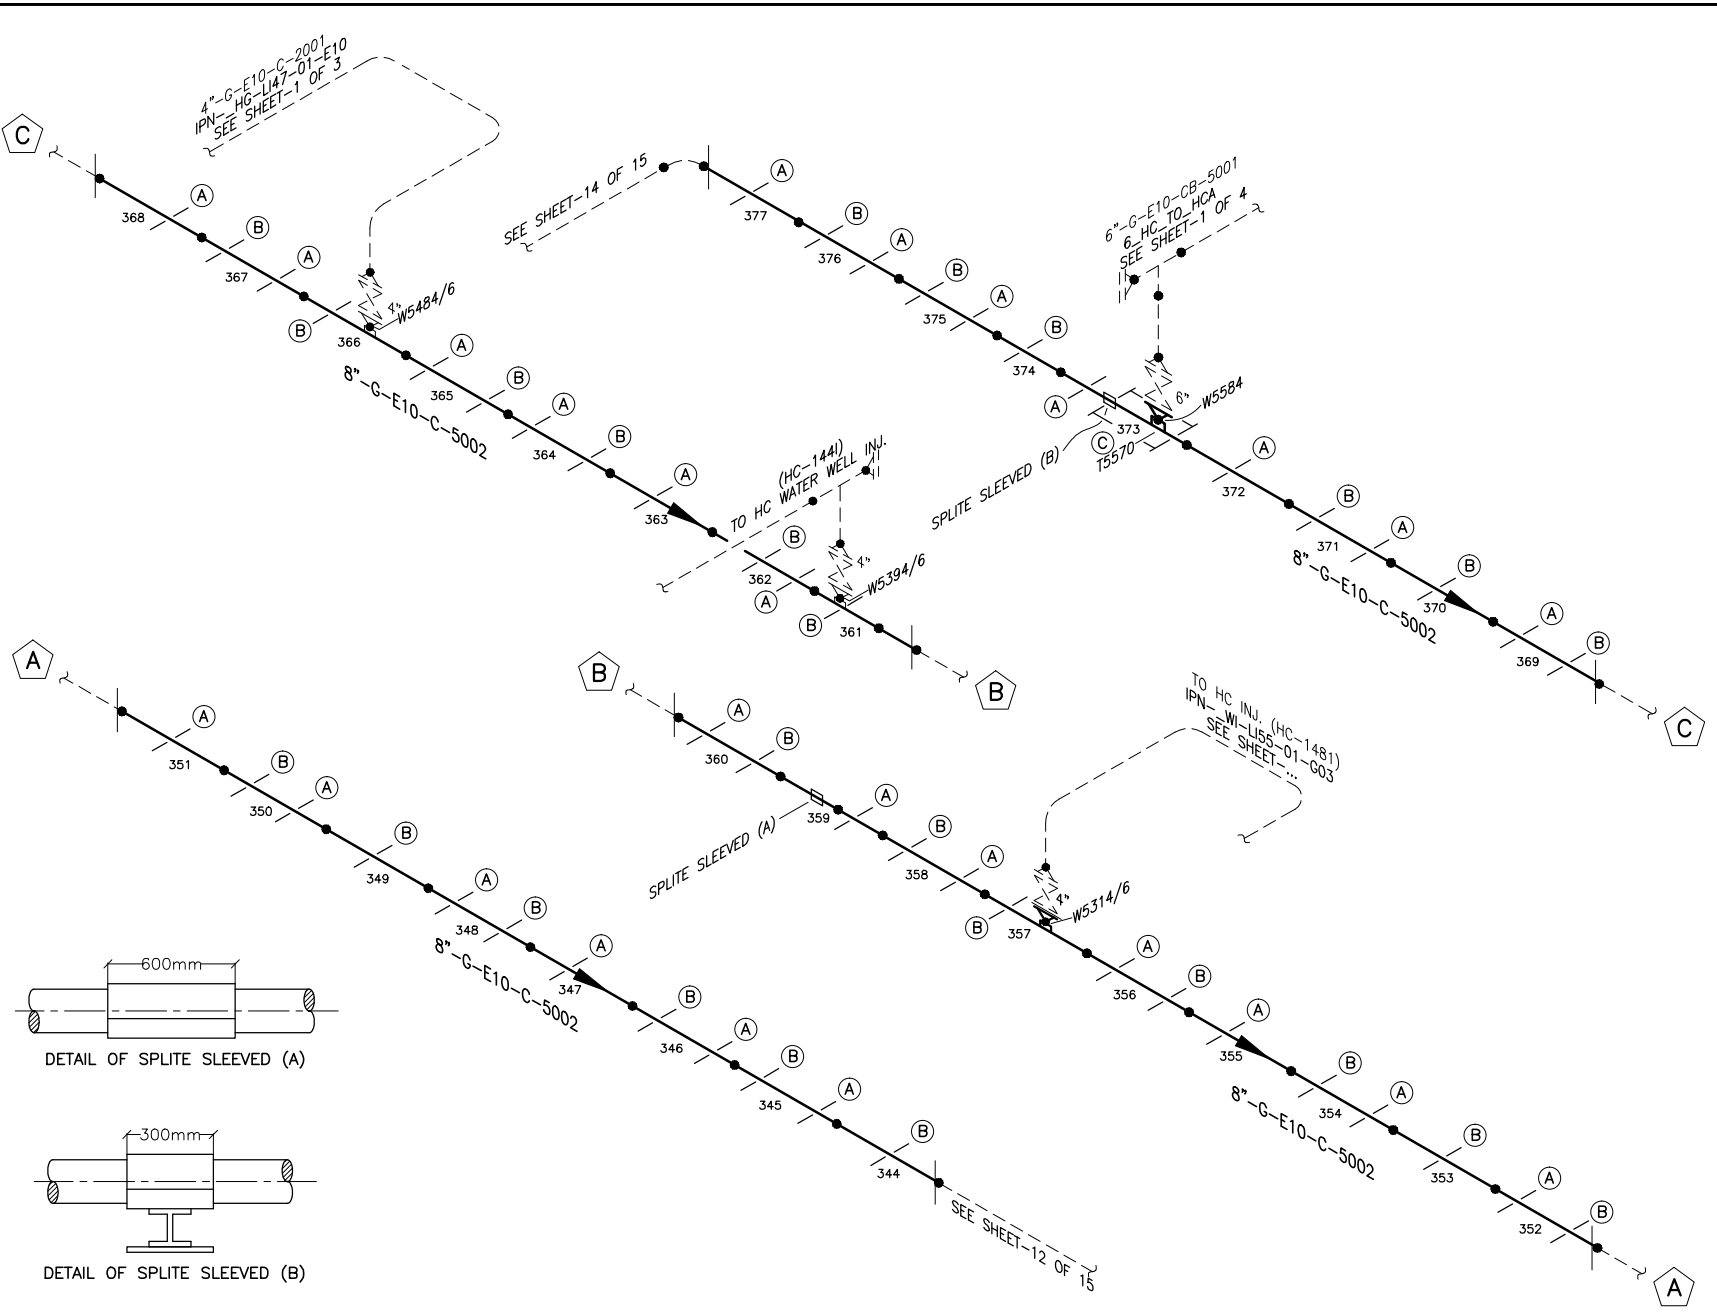
| | | | | | | | | | |
|---|---|---|---|---|---|---|---|---|---|
| | | | | | | | DESIGNED : | OLD TAG. | M3 SOUTH GATHERING LINE |
| | | 5 | 10-01-22 | DST | FBI | | MODIF. DWG MDU 2022-PEP-003 | DRAWN : ROY : 30-11-2005 | |
| | | 4 | 30-07-20 | NAM | FBI | | MODIF. DWG. BASED ON MDU | CHECKED : | NEW TAG. |
| | | 3 | 26-11-14 | ALN | | | CHANGE FUNC. LOCATION | APPROVED : | 8_CPA_TO_HU (PIPELINE) |
| | | 2 | 08-04-14 | SBR | | | MODIF. DWG. BASED ON WO.8206977 | APPROVED : | (M3HYB CLUSTER) |
| P&ID | HDF-12-3570 (1 OF 4/REV-3) | 1 | 27-04-06 | SBR | | | MODIFICATION POINT NUMBER | FILE NAME : 8_HU_TO_CPA-11 | |
| DWG.No. | SUBJECT | No. | DATE | BY | CHK'D/SIGN. | | DESCRIPTION | PERTAMINA HULU MAHAKAM | SCALE NTS / DWG. No. / SHEET 5 11 OF 15 / REV. 5 |
| REFERENCE DRAWINGS | | REVISIONS | | | | | | | |

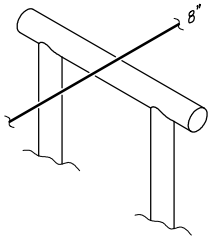
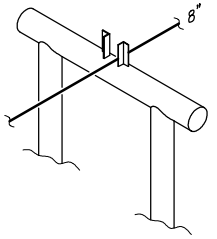
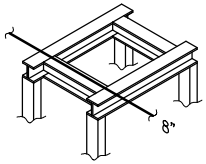



| No | SUPPORT DETAIL |
|---|---|
| A |  |
| B |  |
| C |  |

| CODE | DESCRIPTION |
|---|---|
| AA | NO SPACE FOR SCANNING |
| AC | BLOCKED BY EQUIPMENT |
| AD | BLOCKED BY SUPPORT (cannot be removed) |
| BA | HIGH LOCATION |
| BB | UNDER DECK |
| BC | LAYING PIPE |
| EA | UNDER GROUND |

| | | | | | | | | | |
|---|---|---|---|---|---|---|---|---|---|
| | | | | | | | DESIGNED : | OLD TAG. | M3 SOUTH GATHERING LINE |
| | | 5 | 10-01-22 | DST | FBI | | MODIF. DWG MDU 2022-PEP-003 | DRAWN : ROY : 30-11-2005 | |
| | | 4 | 30-07-20 | NAM | FBI | | MODIF. DWG. BASED ON MDU | CHECKED : | NEW TAG. |
| | | 3 | 26-11-14 | ALN | | | CHANGE FUNC. LOCATION | APPROVED : | 8_CPA_TO_HU (PIPELINE) |
| | | 2 | 08-04-14 | SBR | | | MODIF. DWG. BASED ON WO.8206977 | APPROVED : | (M3HY CLUSTER) |
| P&ID | HDF-12-3580 (1 OF 3/REV-4) | 1 | 27-04-06 | SBR | | | MODIFICATION POINT NUMBER | FILE NAME : 8_HU_TO_CPA-12 | |
| DWG.No. | SUBJECT | No. | DATE | BY | CHK'D/SIGN. | | DESCRIPTION | PERTAMINA HULU MAHAKAM | SCALE NTS / DWG. No. / SHEET 12 OF 15 / REV. 5 |
| REFERENCE DRAWINGS | | REVISIONS | | | | | | | |




| No | SUPPORT DETAIL |
|---|---|
| A |  |
| B |  |
| C |  |

| CODE | DESCRIPTION |
|---|---|
| AA | NO SPACE FOR SCANNING |
| AC | BLOCKED BY EQUIPMENT |
| AD | BLOCKED BY SUPPORT (cannot be removed) |
| BA | HIGH LOCATION |
| BB | UNDER DECK |
| BC | LAYING PIPE |
| EA | UNDER GROUND |

| | | No. | DATE | BY | CHK'D/SIGN. | DESCRIPTION |
|---|---|---|---|---|---|---|
| | | 7 | 10-01-22 | DST | FBI | MODIF. DWG MDU 2022-PEP-003 |
| | | 6 | 30-07-20 | NAM | FBI | MODIF. DWG. BASED ON MDU |
| | | 5 | 02-07-18 | DST | FBI | RE-GROUPING BASED ON MARKUP P&ID |
| | | 4 | 26-11-14 | ALN | | CHANGE FUNC. LOCATION |
| | | 3 | 08-04-14 | SBR | | MODIF. DWG. BASED ON WO.8206977 |
| P&ID | HDF-12-3610 (1 OF 6/REV-4) | 2 | 01-05-09 | ALN | | MOD. DWG BASED ON NOTIF. NO. 14025980 |

REFERENCE DRAWINGS

REVISIONS

DESIGNED :
DRAWN : IRM : 01-12-2005
CHECKED :
APPROVED :
APPROVED :
FILE NAME : 8_HU_TO_CPA-13

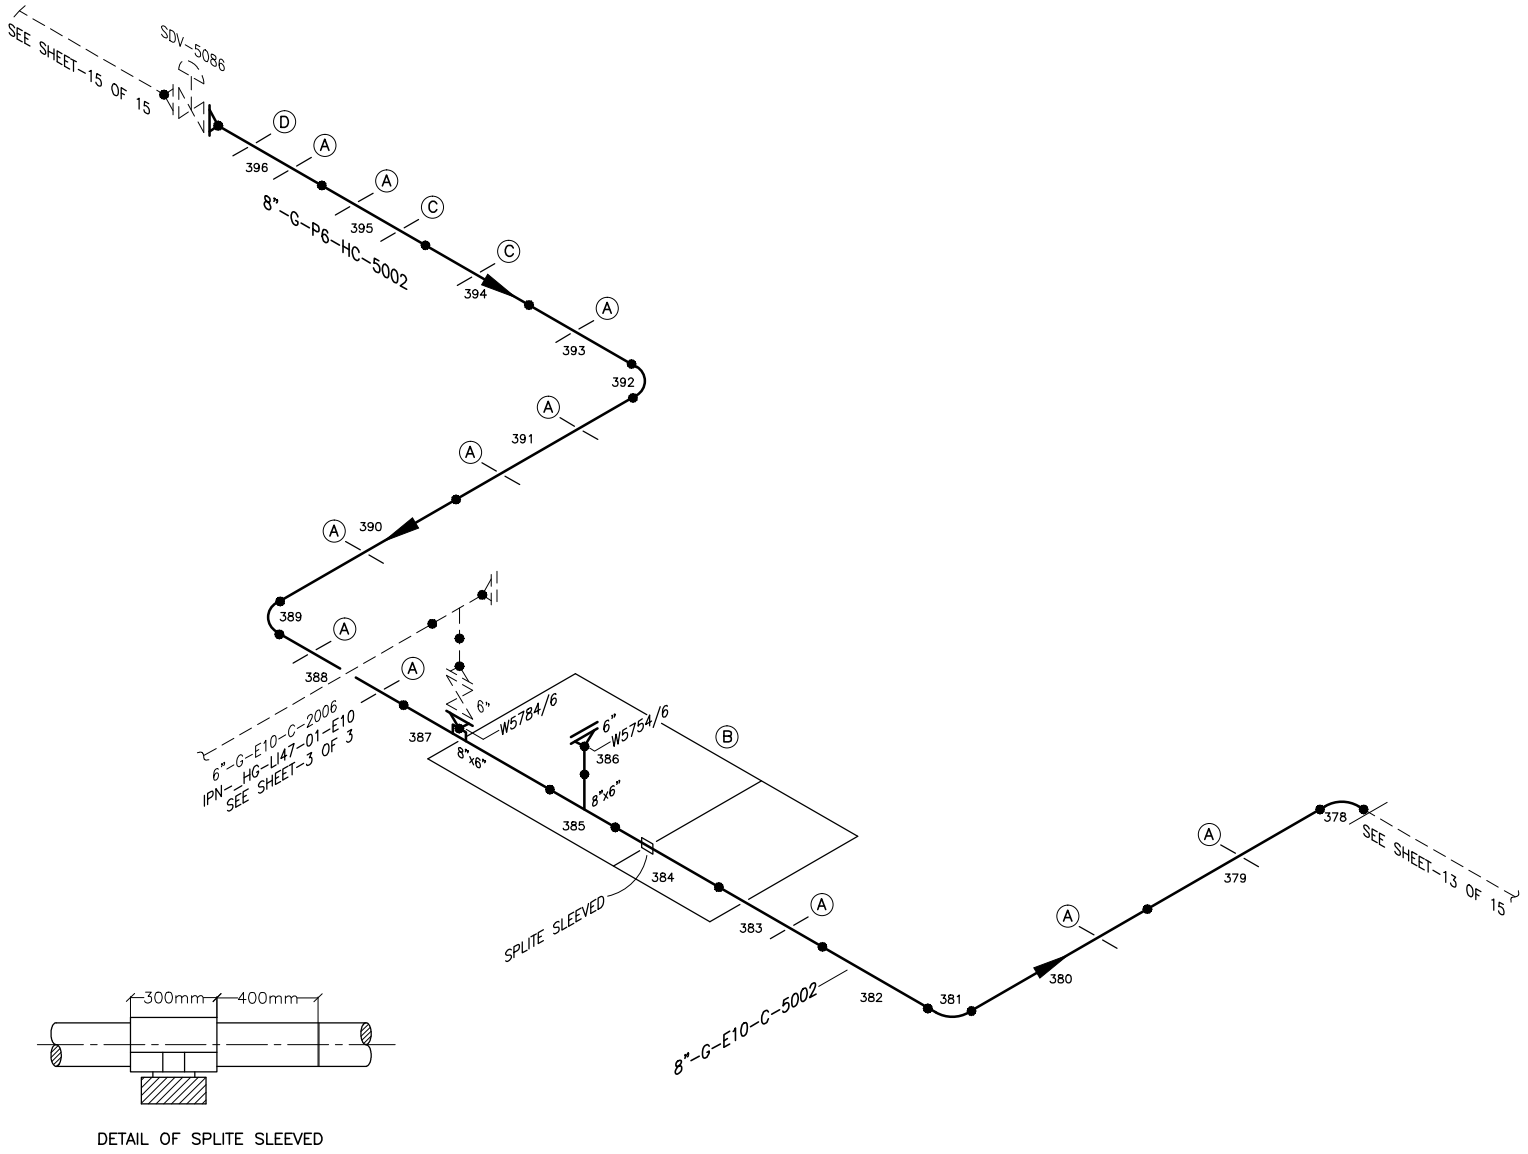
PERTAMINA HULU MAHAKAM

OLD TAG. M3 SOUTH GATHERING LINE

NEW TAG. 8_CPA_TO_HU (PIPELINE)

(M3HC CLUSTER)

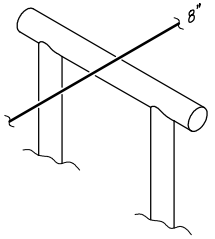
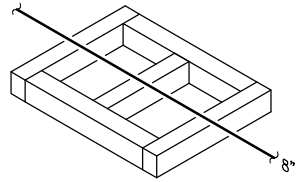
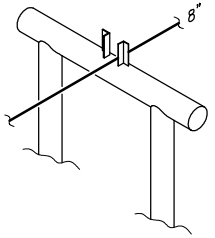
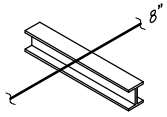
SCALE NTS | DWG. No. | SHEET 7 13 OF 15 | REV. 7







DETAIL OF SPLITE SLEEVED

| No | SUPPORT DETAIL |
|---|---|
| A |  |
| B |  |
| C |  |
| D |  |

| CODE | DESCRIPTION |
|---|---|
| AA | NO SPACE FOR SCANNING |
| AC | BLOCKED BY EQUIPMENT |
| AD | BLOCKED BY SUPPORT (cannot be removed) |
| BA | HIGH LOCATION |
| BB | UNDER DECK |
| BC | LAYING PIPE |
| EA | UNDER GROUND |

| DWG.No. | SUBJECT |
|---|---|
| | |
| | |
| | |
| | |
| P&ID | HDF-12-3610- (1 OF 6/REV-7) |
| P&ID | HDF-12-3611 (1 OF 4/REV-4) |

REFERENCE DRAWINGS

| No. | DATE | BY | CHK'D/SIGN. | DESCRIPTION |
|---|---|---|---|---|
| 7 | 10-01-22 | DST | FBI | MODIF. DWG MDU 2022-PEP-003 |
| 6 | 30-07-20 | NAM | FBI | MODIF. DWG. BASED ON MDU |
| 5 | 02-07-18 | DST | FBI | RE-GROUPING BASED ON MARKUP P&ID |
| 4 | 26-11-14 | ALN | | CHANGE FUNC. LOCATION |
| 3 | 08-04-14 | SBR | | MODIF. DWG. BASED ON WO.8206977 |
| 2 | 19-12-08 | SBR | | MODIFICATION DRAWING |

REVISIONS

DESIGNED :
DRAWN : IRM : 01-12-2005
CHECKED :
APPROVED :
APPROVED :
FILE NAME : 8_HU_TO_CPA-14

PERTAMINA HULU MAHAKAM

OLD TAG.
NEW TAG.

# M3 SOUTH GATHERING LINE

## 8_CPA_TO_HU
(PIPELINE)

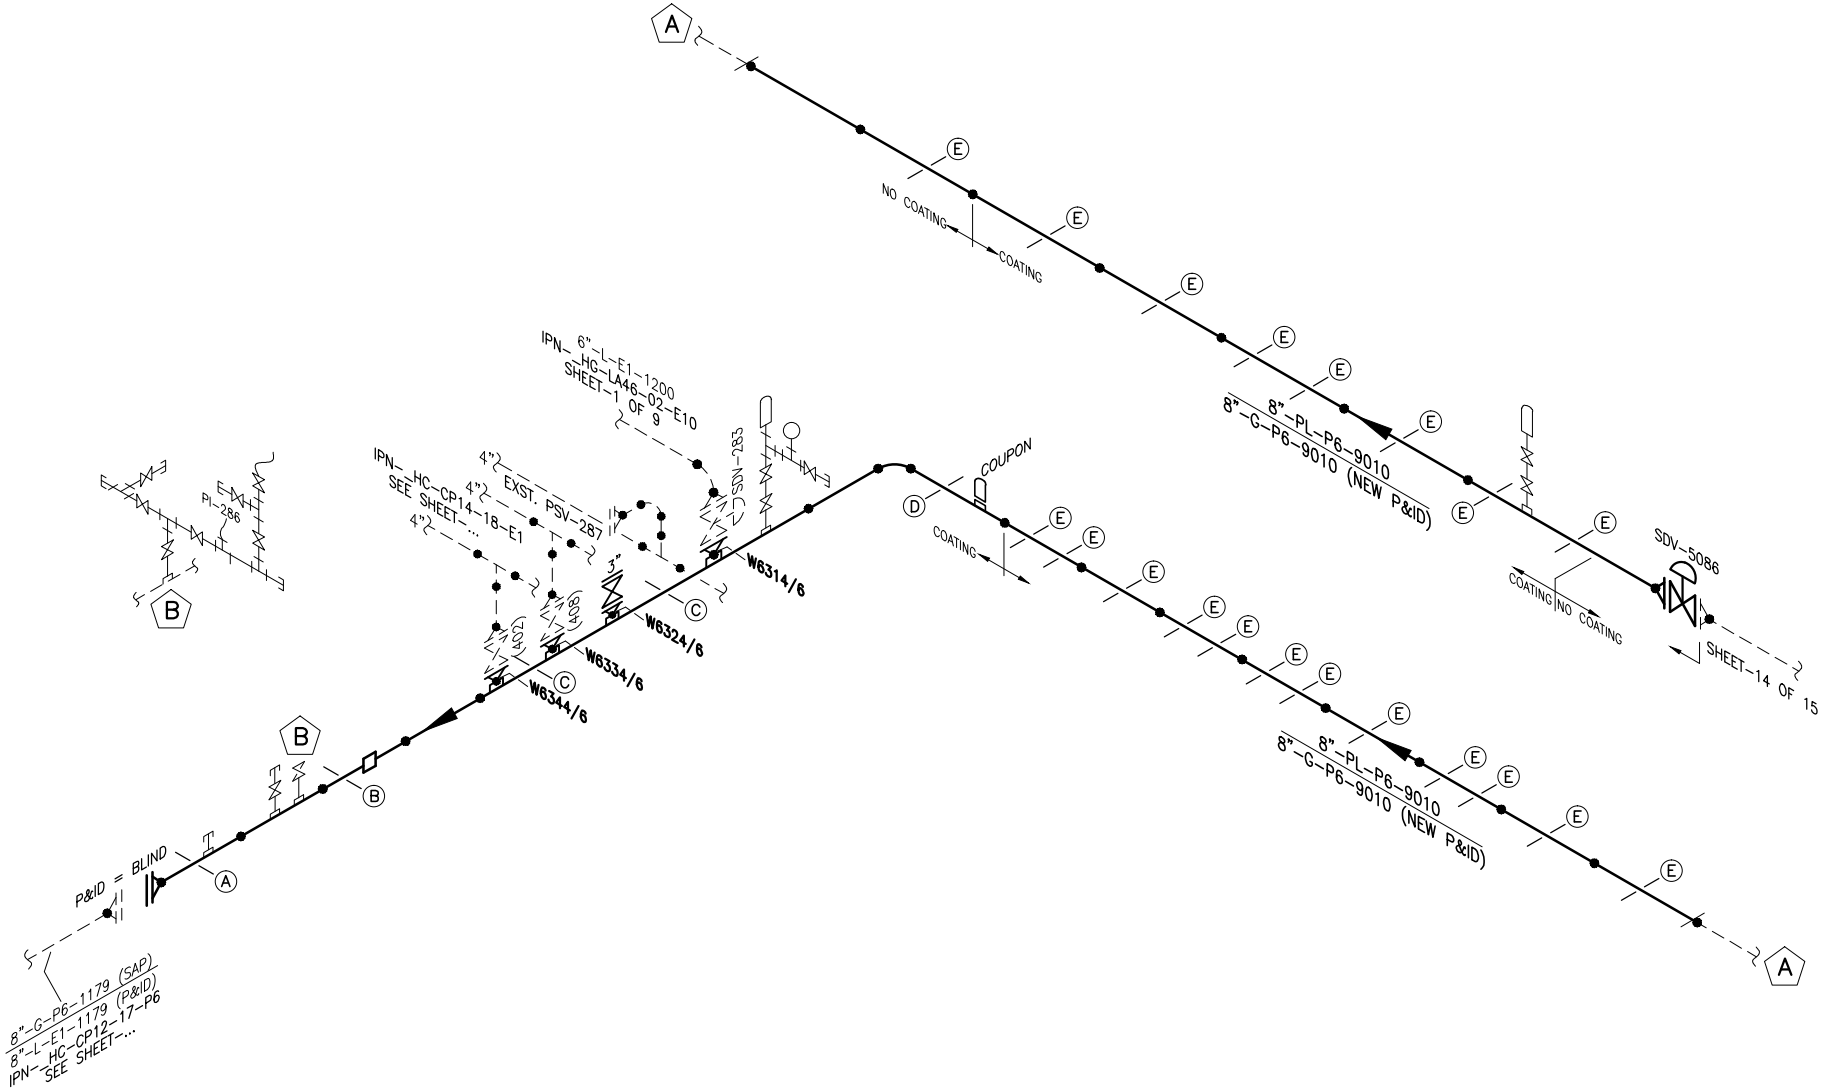
(M3HC CLUSTER & CPA)

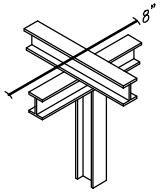
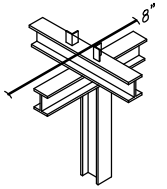
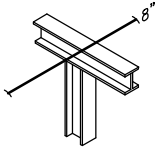
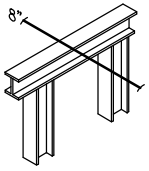
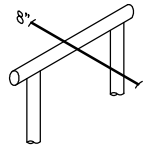
SCALE NTS

DWG. No.

SHEET 7
14 OF 15

REV. 7




| No | SUPPORT DETAIL |
|---|---|
| A |  |
| B |  |
| C |  |
| D |  |
| E |  |

| CODE | DESCRIPTION |
|---|---|
| AA | NO SPACE FOR SCANNING |
| AC | BLOCKED BY EQUIPMENT |
| AD | BLOCKED BY SUPPORT (cannot be removed) |
| BA | HIGH LOCATION |
| BB | UNDER DECK |
| BC | LAYING PIPE |
| EA | UNDERGROUND |

| | | | | | | | | | |
|---|---|---|---|---|---|---|---|---|---|
| | | 9 | 10-01-22 | DST | FBI | | MODIF. DWG MDU 2022-PEP-003 | DESIGNED : | OLD TAG. IPN-_HG-CP41-12-P6 |
| | | 8 | 03-08-20 | NAM | | | MODIF. DRAWING BASED ON MDU | DRAWN : SBR : 23-02-2000 | |
| | | 7 | 04-04-16 | ISK | | | MODIFY IDW AS PER RESULT WO.8364227 | CHECKED : HRN | NEW TAG. 8_CPA_TO_HU (PIPELINE) 9 |
| | | 6 | 22-10-14 | SBR | | | MODIF. DRAWING BASED ON WO.8192452 | APPROVED : | |
| P&ID | CPA-10-1005 (2 OF 71/REV-14) | 5 | 04-01-13 | IMN | | | REVISI DRAWING | APPROVED : | (CPA) |
| P&ID | CPA-10-1005 (1 OF 71/REV-12) | 4 | 29-10-12 | SBR | | | MODIF. DRAWING BASED ON WO.8192281 | FILE NAME : 8_CPA_TO_HU-15 | |
| DWG.No. | SUBJECT | No. | DATE | BY | CHK'D/SIGN. | | DESCRIPTION | PERTAMINA HULU MAHAKAM | SCALE NTS / DWG. No. / SHEET 15 OF 15 / REV. 9 |
| REFERENCE DRAWINGS | | REVISIONS | | | | | | | |